가상 마을D 배수로 정비공사

설 계 도

2026. 10

O O 시

가상 마을D 배수로 정비공사
위 치 도



(1공구) OO면 OO리 OO번지 일원 L=128.1m

2026년 건설사업 합동설계반

事業名	年月日	圖面名	가상 마을D 배수로 정비공사			現場實測		圖面作成		檢圖	圖面番戶	一連番戶	이동장 연락처
2026년 건설사업	2026.10.	事項	위 치 도	縮尺	NONE			* * *			A -		

가상 마을D 배수로 정비공사
종평면도


(1/3) S = H 1:500, V 1:100 (A3)

(1 공 구) L=128.1m

OO면 OO리 OO번지 일원

※ 단위 m · 지반고 = 포장 끝 포장면(GPS RTK) · 계획고 = 관저고(관 안쪽 바닥) · * 보간


[평 면 도] S = 1:500 (노선을 측점 거리대로 편 전개 평면)

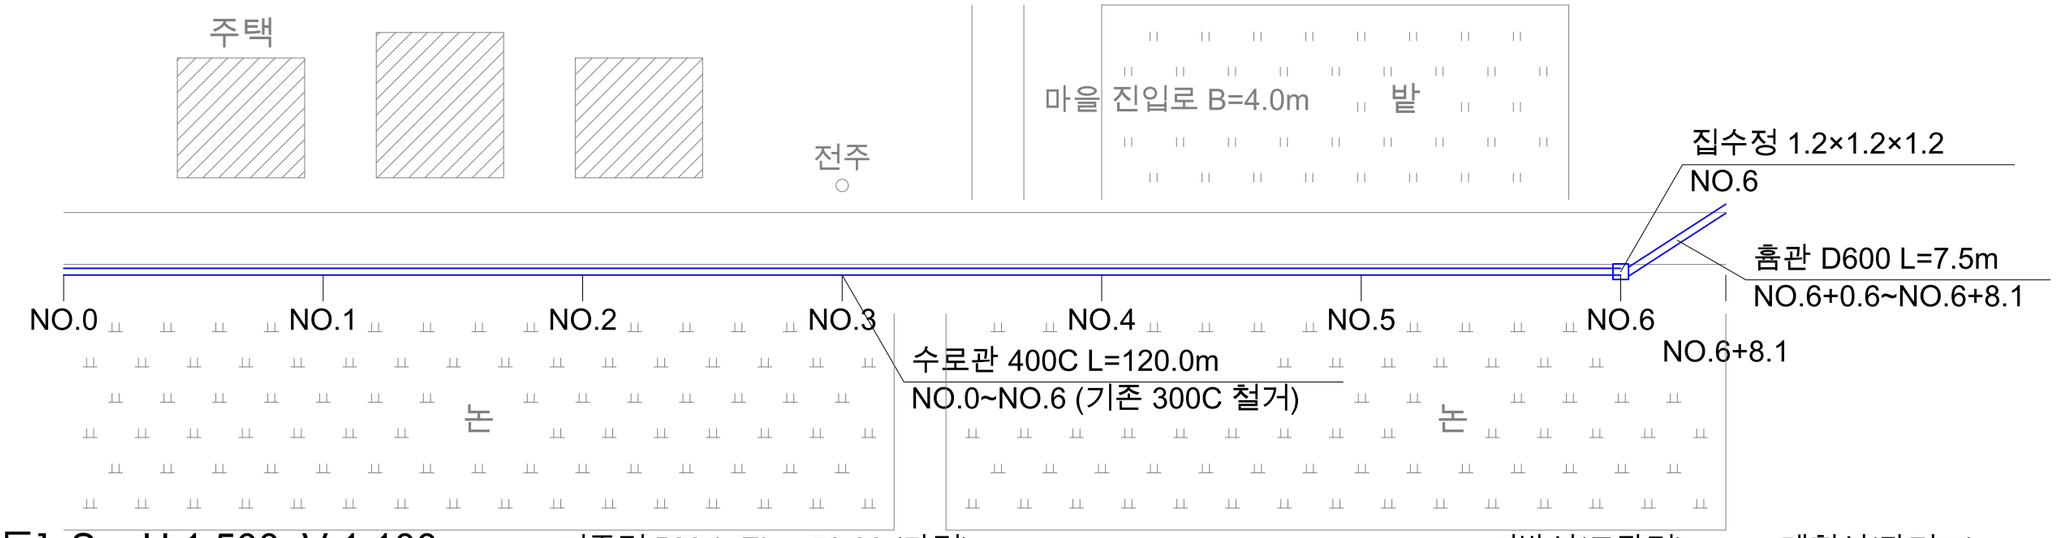

[종 단 면 도] S = H 1:500, V 1:100

기준점 BM.1 EL = 50.00 (가정)

– – – 지반선(포장면) ——— 계획선(관저고) ——— 관 윗면·집수정

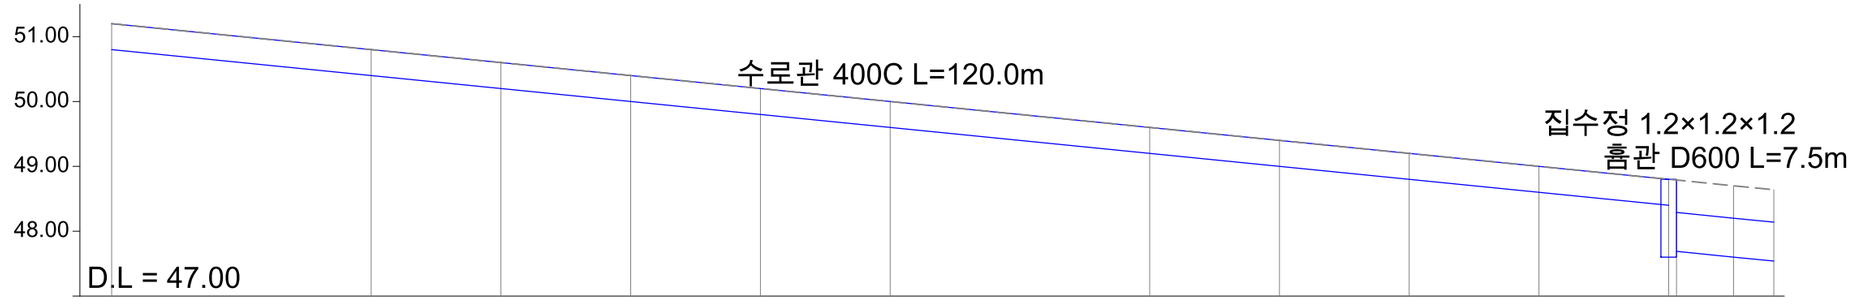

계획경사	i = -2.00% L = 120.0m											-1.98
성 토 고	-	-	-	-	-	-	-	-	-	-	-	-
절 토 고	0.40	0.40	0.40	0.40	0.40	0.40	0.40	0.40	0.40	0.40	0.40	1.10
계 획 고	50.80	50.40	50.20	50.00	49.80	49.60	49.20	49.00	48.80	48.60	48.40	47.54
지 반 고	51.20	50.80	50.60*	50.40	50.20*	50.00	49.60	49.40*	49.20	49.00*	48.80	48.64
누가거리	0.00	20.00	30.00	40.00	50.00	60.00	80.00	90.00	100.00	110.00	120.00	128.10
거 리	0.00	20.00	10.00	10.00	10.00	10.00	20.00	10.00	10.00	10.00	10.00	8.10
측 점	NO.0	NO.1	NO.1 +10	NO.2	NO.2 +10	NO.3	NO.4	NO.4 +10	NO.5	NO.5 +10	NO.6	NO.6 +8.1

2026년 건설사업 합동설계반

事 業 名	年 月 日	圖 面 名	가상 마을D 배수로 정비공사		現 場 實 測		圖 面 作 成		檢 圖	圖面番戶	一連番戶	이동장 연락처
2026년 건설사업	2026.10.	事 項	종 평 면 도	縮 尺 H1:500 V1:100			* * *			A -		


가상 마을D 배수로 정비공사
횡단면도

(2/3) S = 1:50 (A3)


(1 공 구) L=128.1m

OO면 OO리 OO번지 일원


※ 단위 m · 지반선은 야장(상대 깊이) · 같은 단면 측점은 비고에 생략 표기

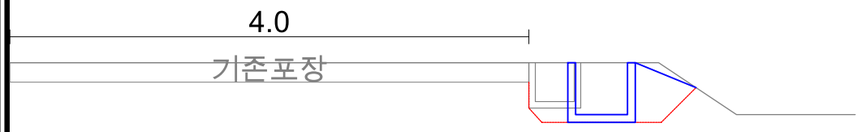

NO.	NO.2	(단위 ㎡)	
터파기	0.38	되메우기	0.27
절 취		비 고	논 0.3m 낮음

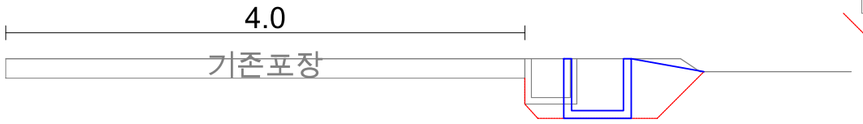

NO.	NO.4+10	(단위 ㎡)	
터파기	0.41	되메우기	0.30
절 취		비 고	진입로 옆 길어깨

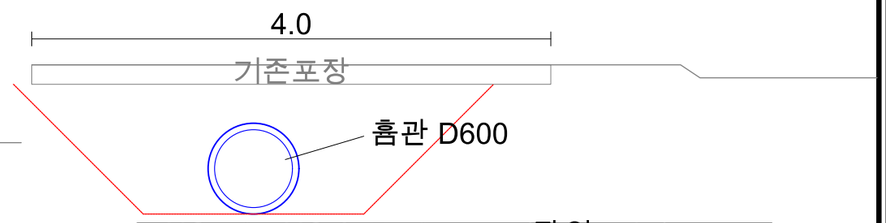


NO.	NO.6+5	(단위 ㎡/m)	
터파기	2.70	되메우기	2.32
절 취		비 고	도로 횡단




NO.	NO.1+10	(단위 ㎡)	
터파기	0.41	되메우기	0.30
절 취		비 고	길어깨 1.2m




NO.	NO.4	(단위 ㎡)	
터파기	0.38	되메우기	0.27
절 취		비 고	논 0.3m 낮음

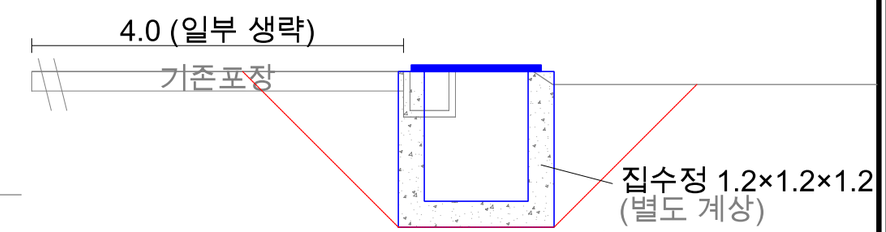


NO.	NO.6	(단위 ㎡)	
터파기	-	되메우기	-
절 취		비 고	종점 집수정

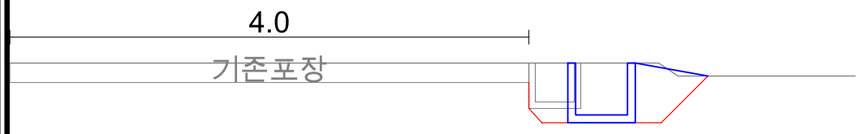


NO.	NO.1	(단위 ㎡)	
터파기	0.39	되메우기	0.30
절 취		비 고	

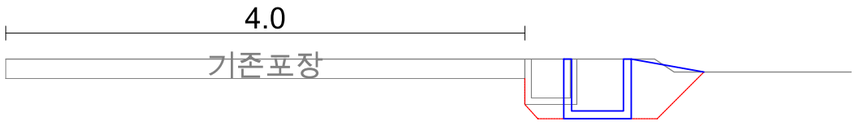


NO.	NO.3	(단위 ㎡)	
터파기	0.39	되메우기	0.30
절 취		비 고	

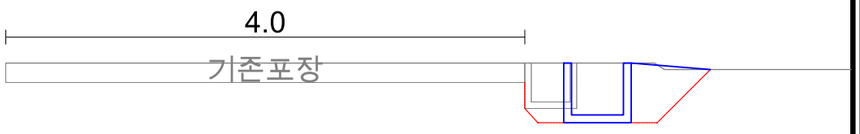


NO.	NO.5+10	(단위 ㎡)	
터파기	0.41	되메우기	0.31
절 취		비 고	논 0.05m 낮음

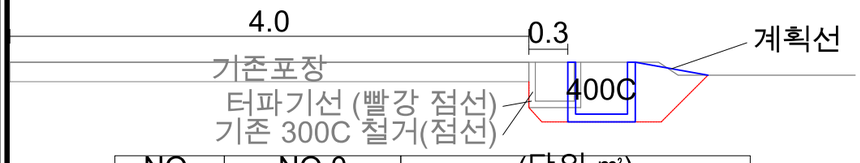

NO.	NO.0	(단위 ㎡)	
터파기	0.39	되메우기	0.30
절 취		비 고	NO.0+10 같음(생략)

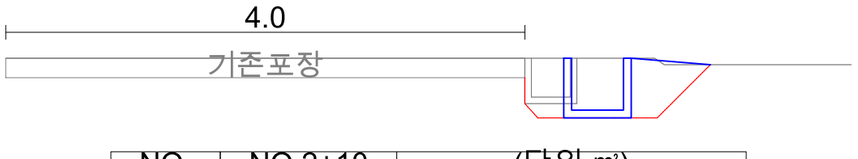

NO.	NO.2+10	(단위 ㎡)	
터파기	0.41	되메우기	0.31
절 취		비 고	논 0.05m 낮음

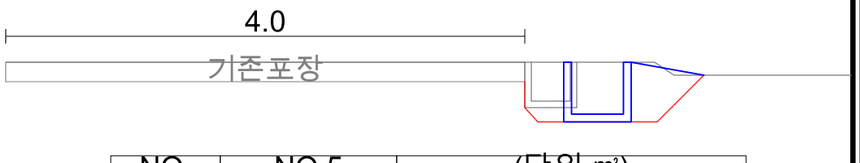

NO.	NO.5	(단위 ㎡)	
터파기	0.39	되메우기	0.30
절 취		비 고	

2026년 건설사업 합동설계반


事 業 名	年 月 日	圖 面 名	가상 마을D 배수로 정비공사		現 場 實 測		圖 面 作 成		檢 圖	圖面番戶	一連番戶	이동장 연락처
2026년 건설사업	2026.10.	事 項	횡 단 면 도	縮 尺 1:50			* * *			A -		

가상 마을D 배수로 정비공사
상세도


(3/3) S = 1:20 (A3)

상세도


U형 수로관 400C

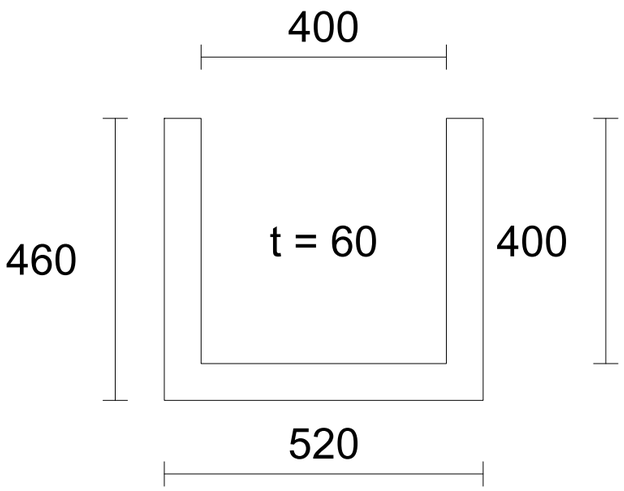

흄관 D600 (고무링 접합)

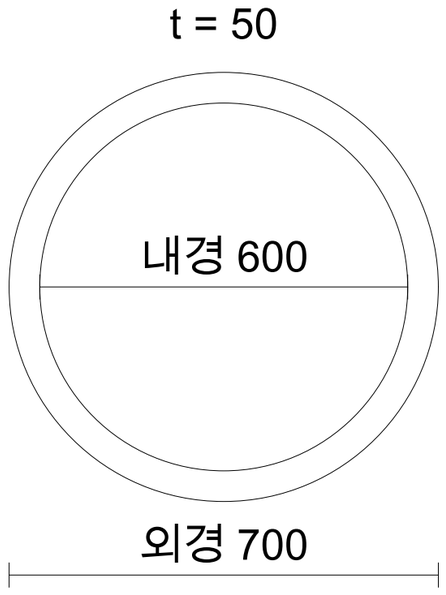

집수정 (단면)

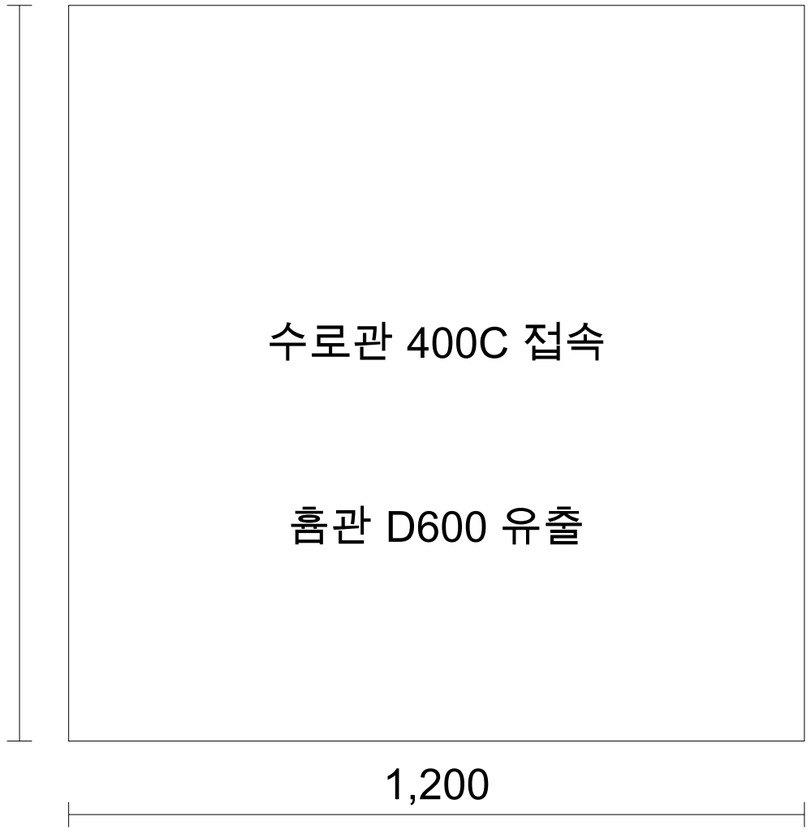

※ 치수 단위 mm — 가상 예제(제품 규격 치수)

2026년 건설사업 합동설계반

事業名	年月日	圖面名	가상 마을D 배수로 정비공사			現場實測		圖面作成		檢圖	圖面番戶	一連番戶	이동장 연락처
2026년 건설사업	2026.10.	事項	상 세 도	縮尺	1:20			***			A -		