

가상 마을D 배수로 정비공사
설 계 도

2026. 10

〇 〇 시

가상 마을D 배수로 정비공사 위 치 도




(1공구) 00면 00리 00번지 일원 L=128.1m

가상 마을D 배수로 정비공사 계획평면도

(1/3) S = 1:400 (A3)

(1 공 구) L=128.1m

00면 00리 00번지 일원

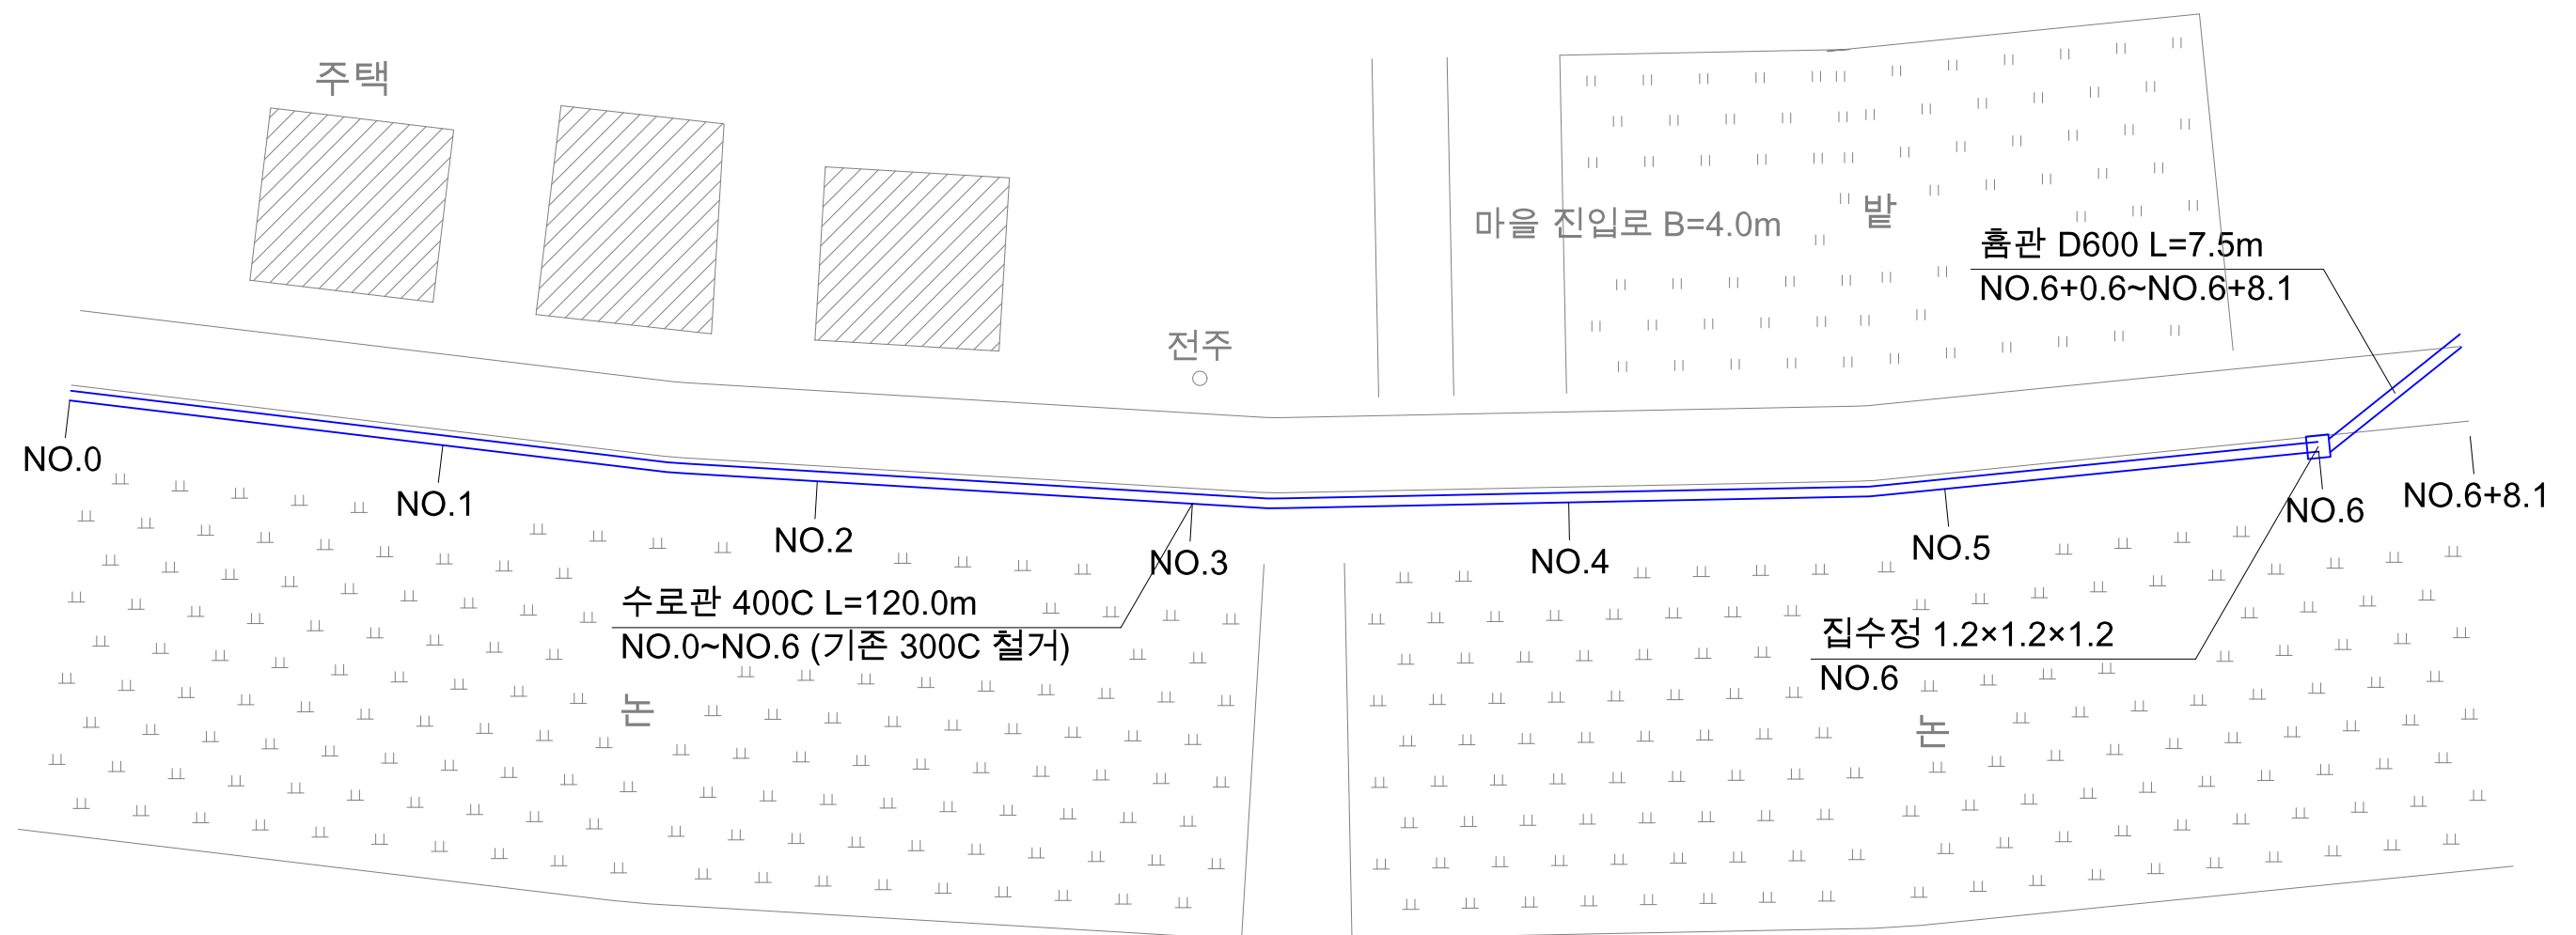

2026년 건설사업 합동설계반

事業名

2026년 건설사업

年月日

2026.10.

圖面名

事項

가상 마을D 배수로 정비공사

계획평면도

縮尺

1:400

現場實測

圖面作成

檢圖

圖面番戶

A -

一連番戶













이동장 연락처

가상 마을D 배수로 정비공사 횡단면도

(2/3) S = 1:50 (A3)

(1 공 구) L=128.1m 00면 00리 00번지 일원

※ 단위 m · 지반선은 야장(상대 깊이) · 같은 단면 측점은 비교에 생략 표기

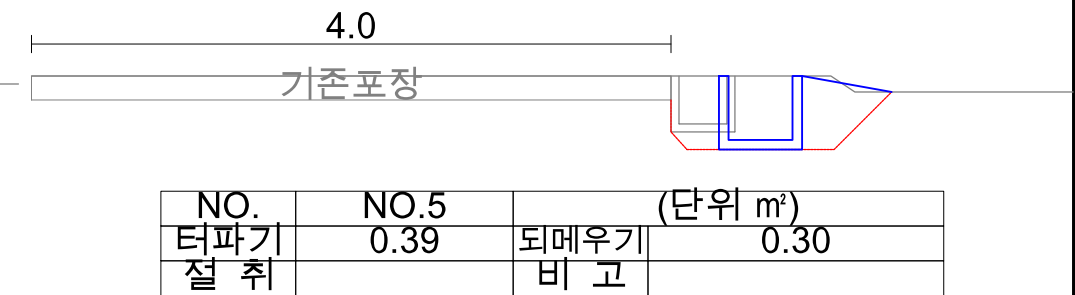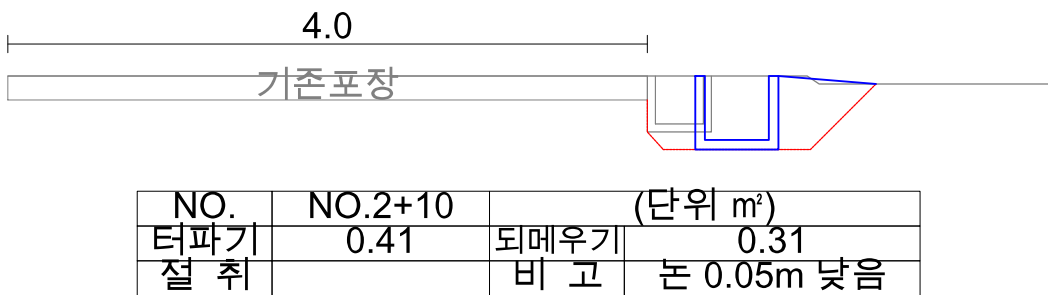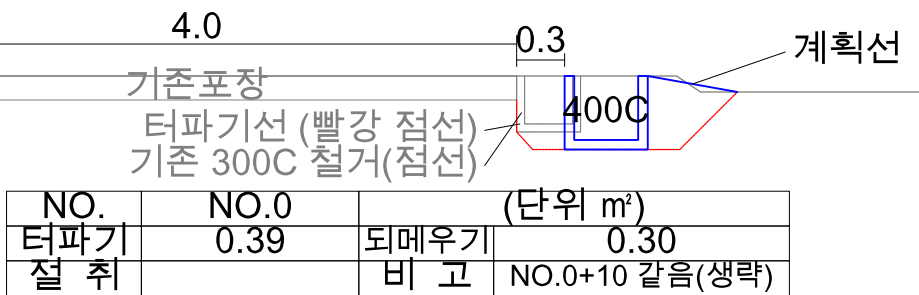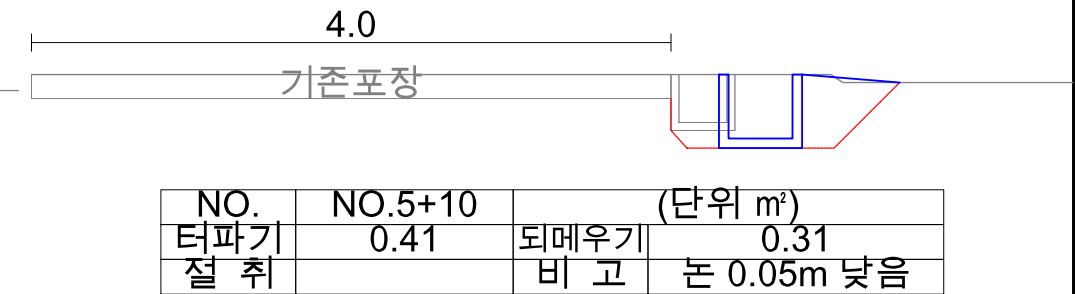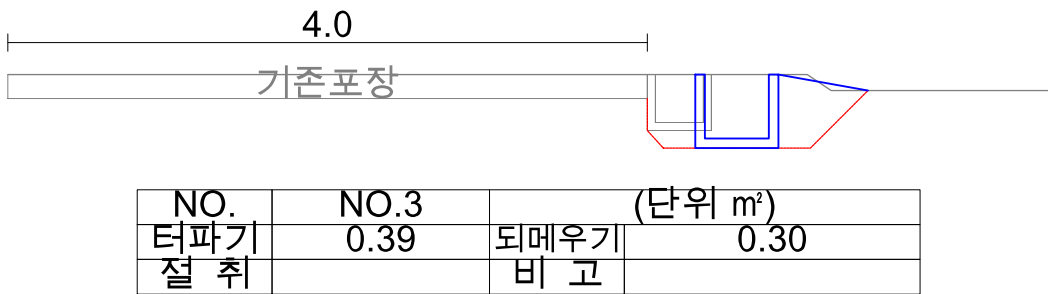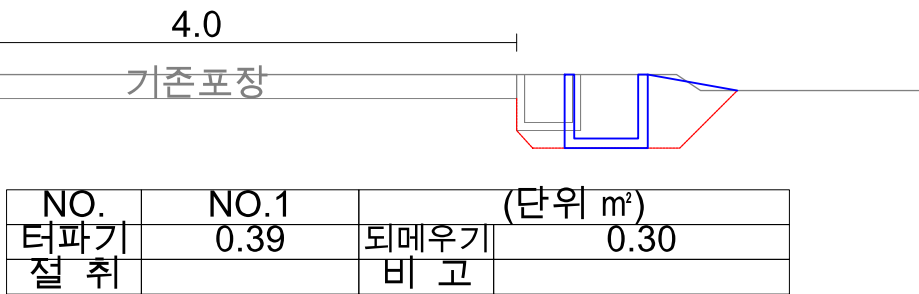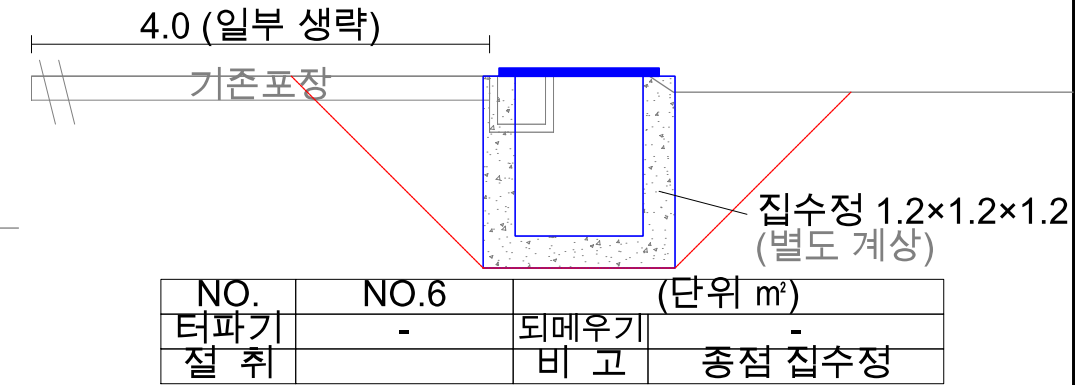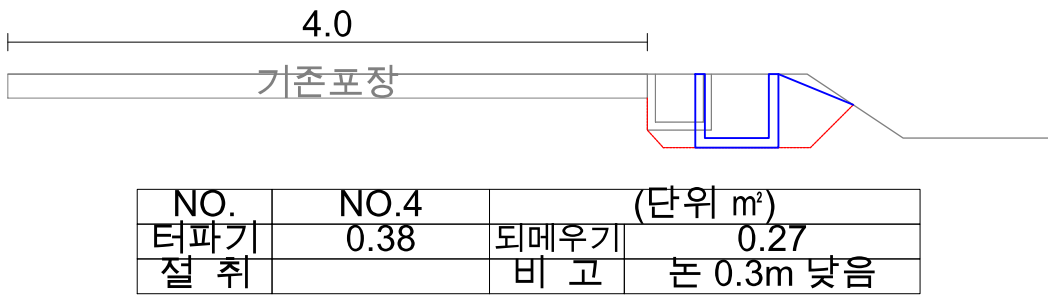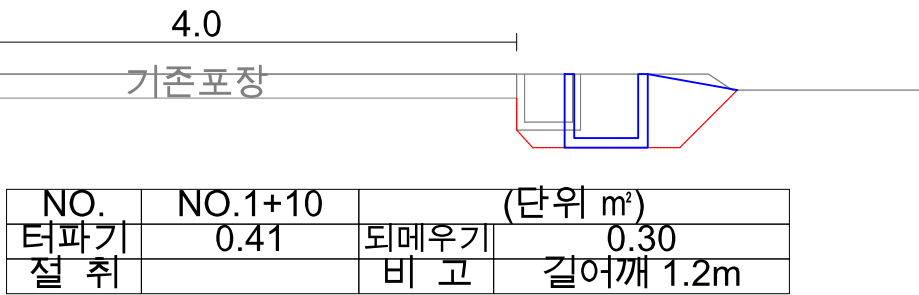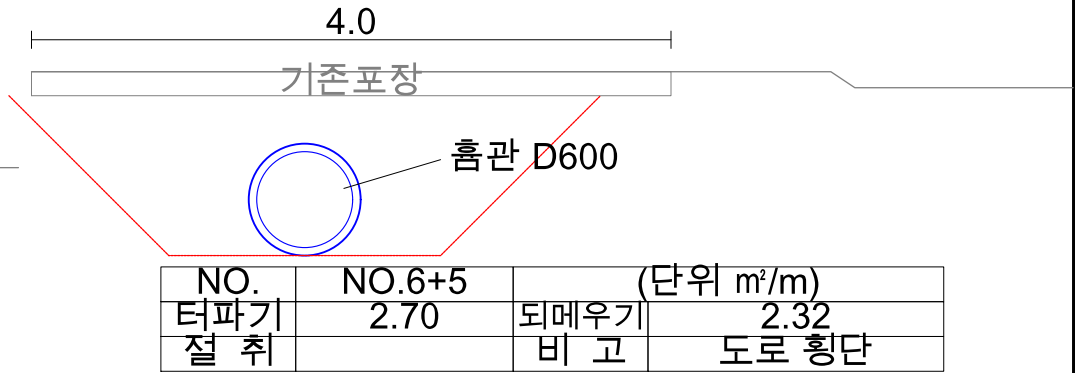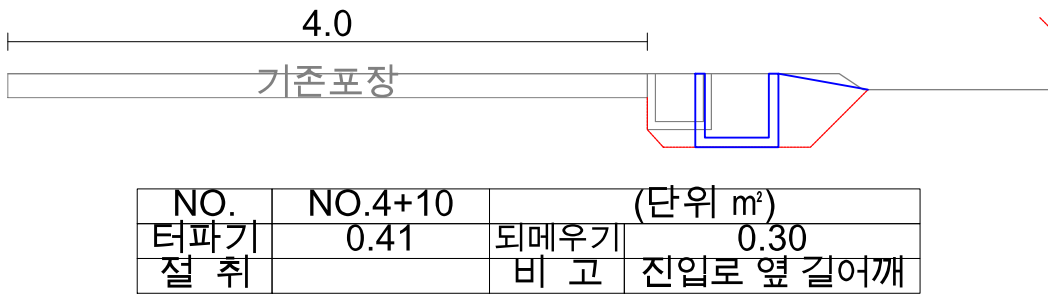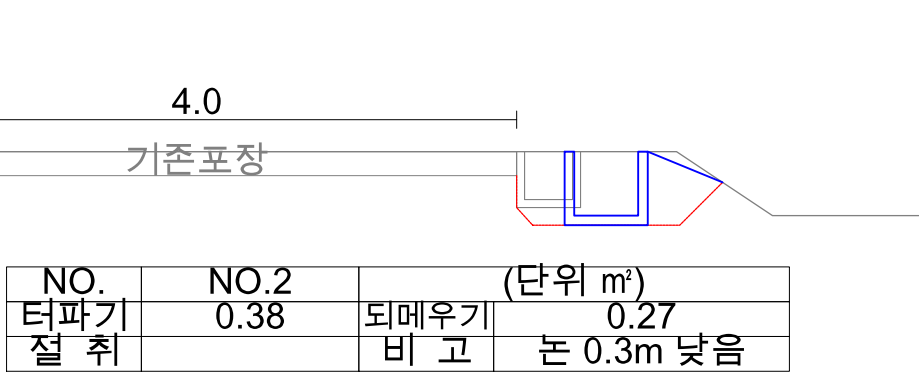

2026년 건설사업 합동설계반


事業名	年月日	圖面名	現場實測	圖面作成	檢圖	圖面番戶	一連番戶	이동장 연락처
2026년 건설사업	2026.10.	事項 횡단면도	縮尺 1:50	***		A-		

가상 마을D 배수로 정비공사
상세도


(3/3) S = 1:20 (A3)

상세도


U형 수로관 400C

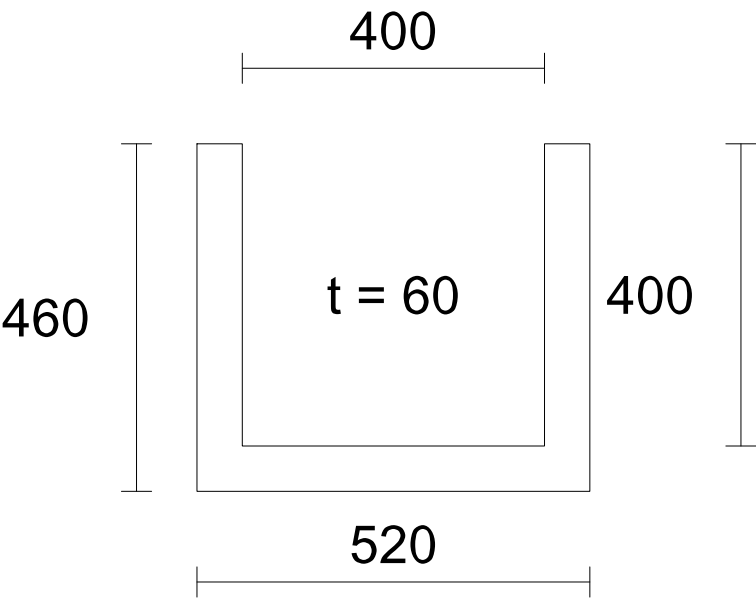

흙관 D600 (고무링 접합)

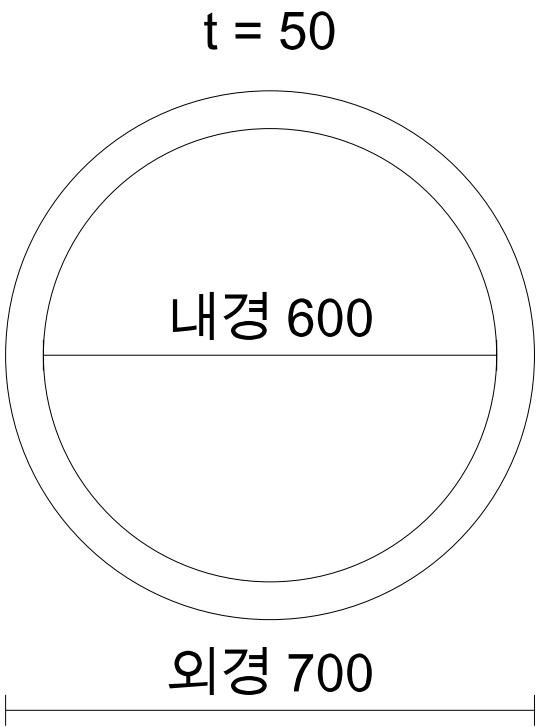

집수정 (단면)

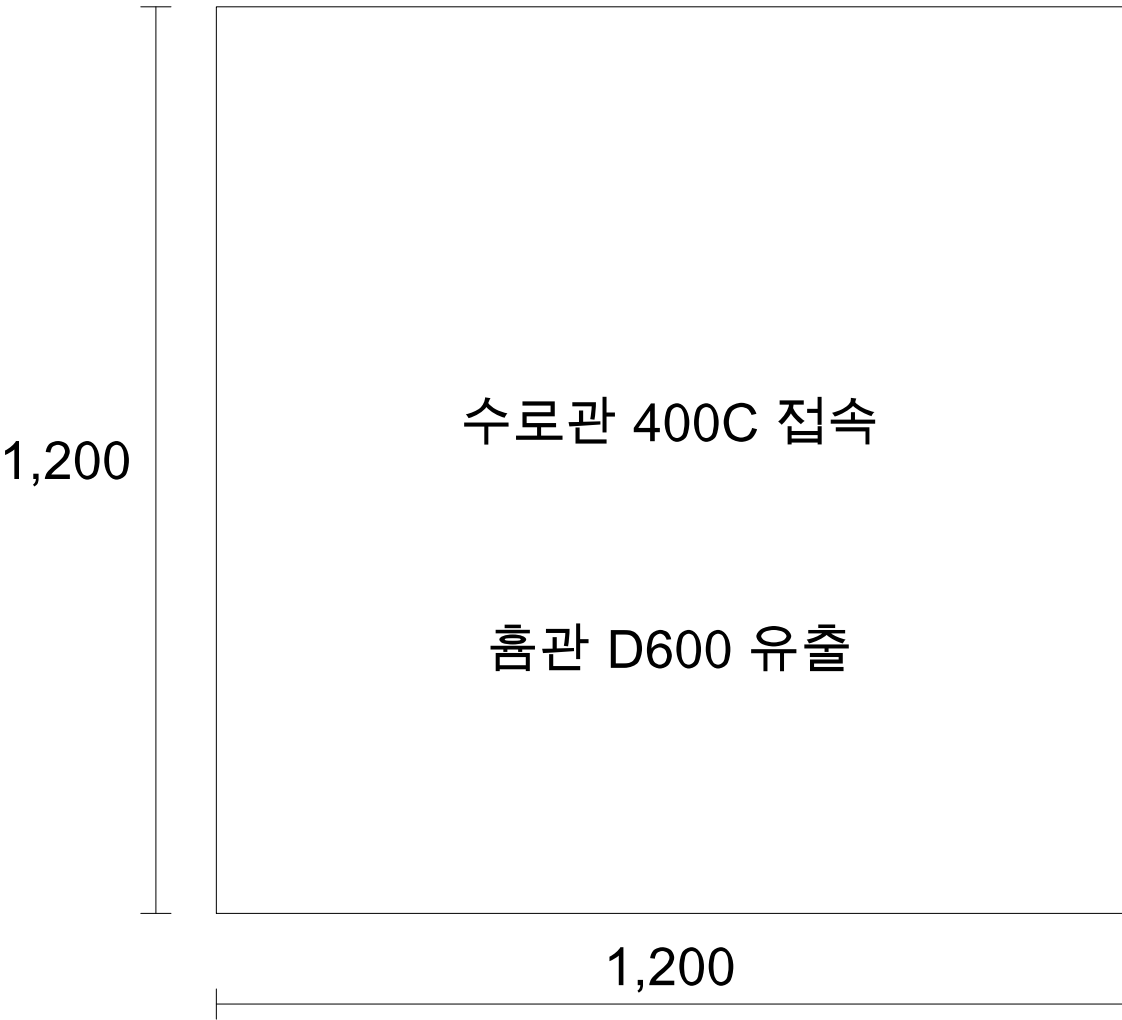

※ 치수 단위 mm — 가상 예제(제품 규격 치수)