

가상 마을E 소하천 호안 정비공사

설 계 도

2026. 10

〇 〇 시

가상 마을E 소하천 호안 정비공사
위 치 도



OO면 OO리 OO번지 지내 식생블럭 L=24.0m, H=2.0m

事業名	年月日	圖面名	가상 마을E 소하천 호안 정비공사	現場實測	圖面作成	檢圖	圖面番戶	一連番戶	이동장 연락처
2026년 건설사업	2026.10.	事項	위 치 도	縮尺	NONE		***	A -	


가상 마을E 소하천 호안 정비공사 평면도 · 정면도

평면 S = 1:200 · 정면 S = 가로 1:200, 세로 1:100


(호 안 공) L=24.0m H=2.0m (4단)

OO면 OO리 OO번지 지내

[평면도]

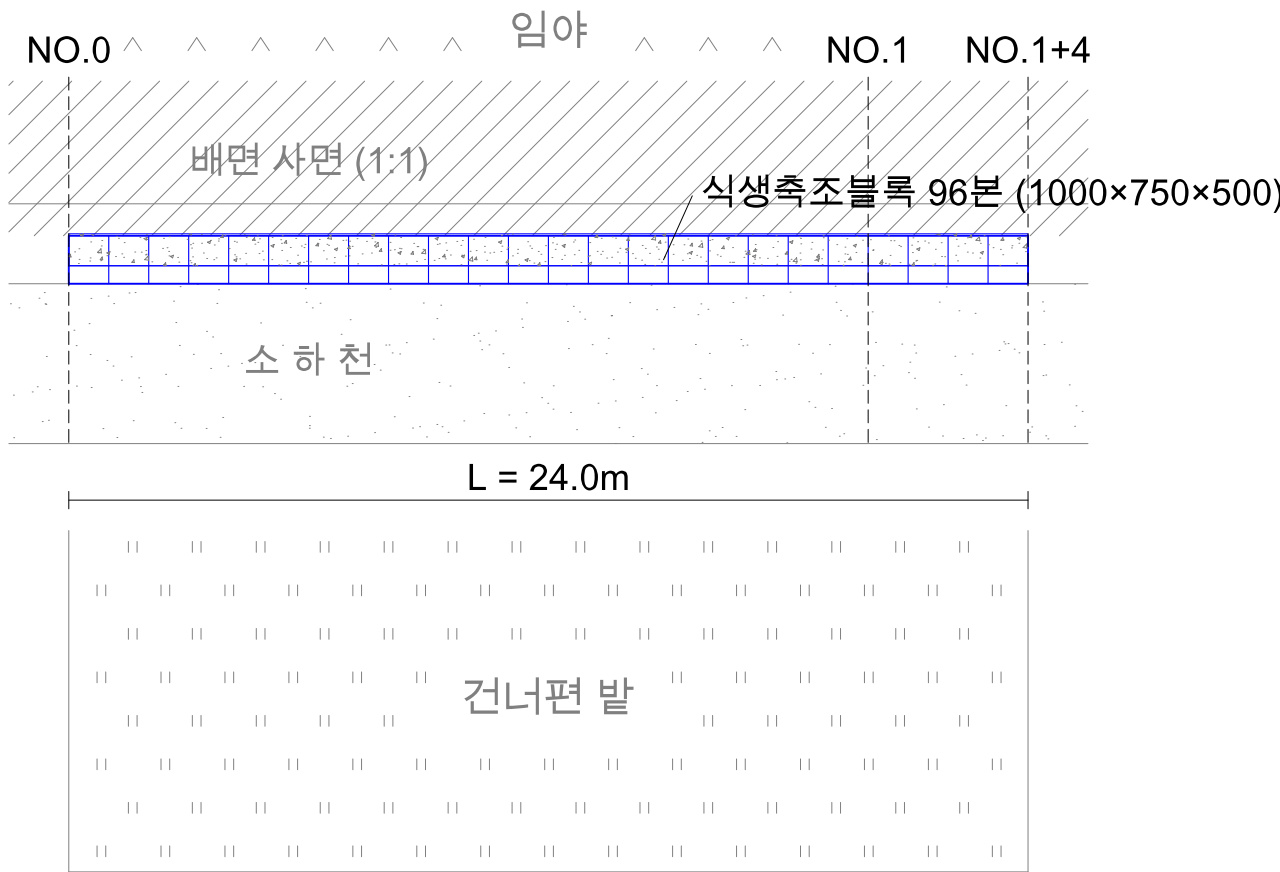

[정면도] (전면에서 봄, 세로 2배)

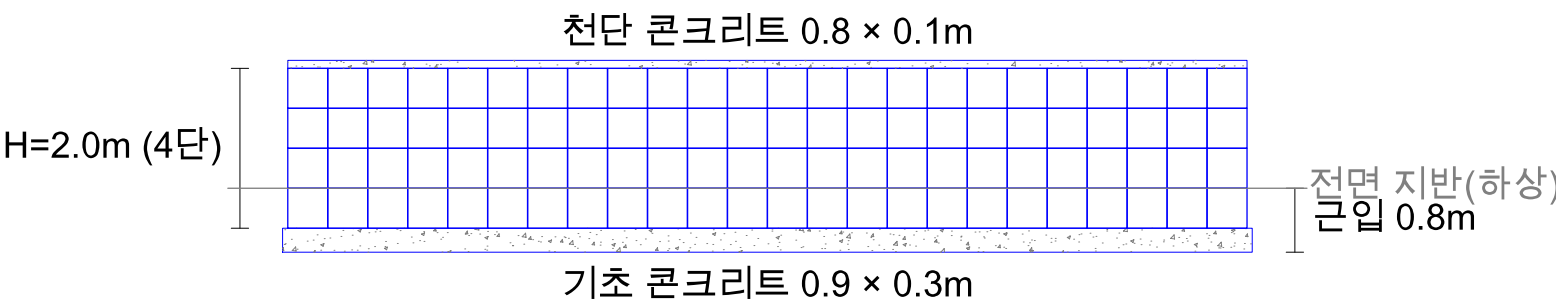

- 기존 지반·시설 (회색)
- 터파기선 (1:1)
- 부직포 (흡출방지)
- ▨ 뒹채움 쇠골재 25mm
- ▨ 기초·천단 콘크리트
- 식생축조블록 (신설)

[범례]

식생블럭
식생축조블록 1000×750×500 96본
L=24.0m, H=2.0m (4단, 1단 근입), A=48.0㎡
기초·천단
기초 0.9×0.3m, 천단 0.8×0.1m (25-18-8)
기초 거푸집 합판 6회, 천단 유로폼
뒹채움
쇠골재 25mm (속채움·뒹채움)
부직포 흡출방지 A=50.2㎡
터파기·잔토
기초 바닥 양 끝에서 1:1 (여유 0.5m)
잔토 현장갈기
블럭 형상은 제조사 표준도 기준

[NOTE]

2026년 건설사업 합동설계반

事業名	年月日	圖面名	現場實測	圖面作成	檢圖	圖面番戶	一連番戶	이동장 연락처
2026년 건설사업	2026.10.	가상 마을E 소하천 호안 정비공사 평면도	縮尺 1:200	***		A -		


횡단면도 · 상세도

횡단 S = 1:50 · 상세 S = 1:25

(호안공) L=24.0m H=2.0m (4단)

00면 00리 00번지 지내

[대표 횡단면도] S=1:50 (NO.0 ~ NO.1+4 같은 단면)

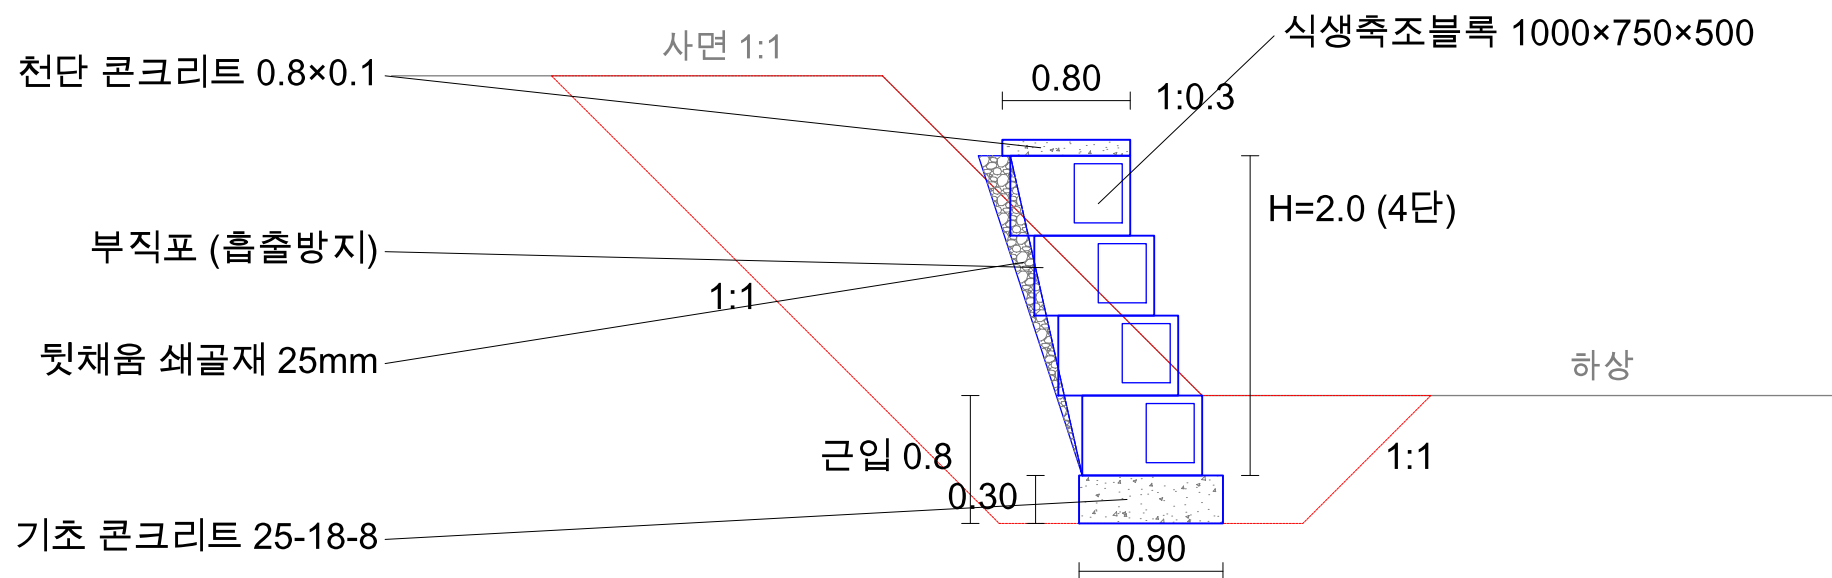


L=24.0 H=2.0m (4단)

[단위수량표] (1m당)

터파기	6.30 m ²	천단 콘크리트	0.08 m ³
되메움	5.08 m ²	속채움 쇠골재	0.24 m ³
잔토(현장깔기)	1.22 m ²	틔채움 쇠골재	0.2 m ³
블럭 높이	H = 2.0m	부직포	2.09 m ²
기초 콘크리트	0.27 m ³	식생블럭	4 본

[블록 상세도] S=1:25

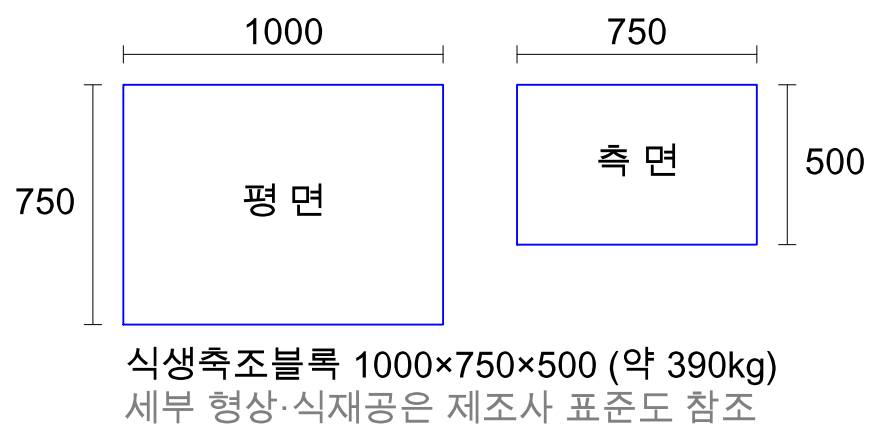

- 기존 지반·시설 (회색)
- 터파기선 (1:1)
- - - 부직포 (흡출방지)
-  틈채움 쇄골재 25mm
-  기초·천단 콘크리트
-  식생축조블록 (신설)

[범례]

블록
4단 쌓기, 단마다 0.15m 물림 (1:0.3)
1단은 전면 지반 아래 근입

기초
0.9×0.3m, 블록 앞굽 0.13m
기초 바닥 = 전면 지반 -0.8m (근입)

시공순서
① 터파기 ② 기초 타설
④ 양생 ⑤ 직포·틔채움·속채움
⑥ 천단 ⑦ 블럭쌓음

안정 검토(간이, $\phi 30^\circ$)
 활동 1.31 · 전도 2.11 · 편심 0.07m (B/6 0.15)
 시행째기($\phi 30^\circ$, $\delta = 2/3\phi$, $c=0$, 상재 0, 활동면 $\geq$ 사면각 45.0°)

안정 검토(간이, $\phi 35^\circ$)
 활동 2.10 · 전도 2.81 · 편심 -0.01m (B/6 0.15)
 시행째기($\phi 35^\circ$, $\delta = 2/3\phi$, $c=0$, 상재 0, 활동면 $\geq$ 사면각 45.0°)

터파기 후 배면 지반 확인, 연약 시 하단 보강(설계변경)

[NOTE]