가상 마을A 마을안길 정비공사

설 계 도

2026. 09

O O 시

가상 마을A 마을안길 정비공사
위　치　도



(1공구) OO면 OO리 OO번지 일원 L=240.0m
(2공구) OO면 OO리 OO번지 일원 L=10.0m


2026년 건설사업 합동설계반


事業名	年月日	圖面名	가상 마을A 마을안길 정비공사		現場實測		圖面作成		檢圖	圖面番戶	一連番戶	이동장 연락처
2026년 건설사업	2026.09.	事項	위 치 도	縮尺 NONE			* * *			A -		

가상 마을A 마을안길 정비공사
아스콘 덧씌우기 전개도

(1/2) S = NONE

(1 공 구) L=240.0m　　OO면 OO리 OO번지 일원

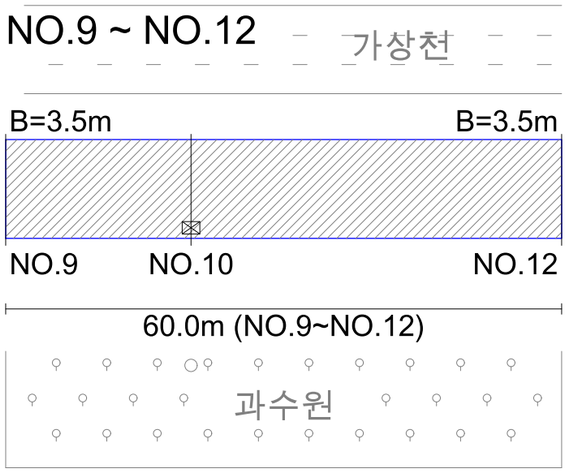

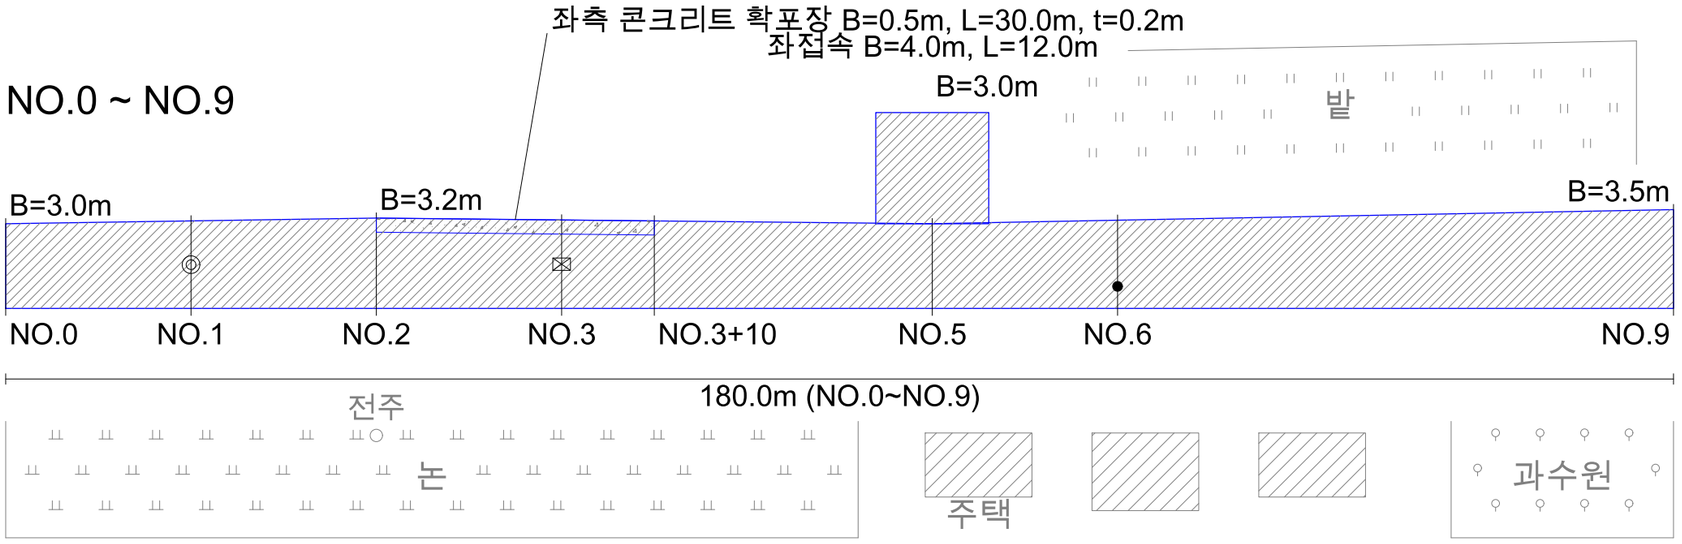

- 집수정 숭상 (1000×600)
- 지수전 숭상 (D150)
- 맨홀 숭상 (D600)
- 콘크리트 확포장 (좌측)
- 아스콘 덧씌우기

[범 례]

NO.0~NO.12
차선도색(백색실선) 양측 L=240.0m

NO.10
집수정(1000×600) 숭상 1EA

NO.6
지수전(D150) 숭상 1EA

NO.5
좌접속 아스콘 B=4.0m, L=12.0m

NO.3
집수정(1000×600) 숭상 1EA

NO.2~NO.3+10
좌측 콘크리트 확포장 B=0.5m, L=30.0m
t=0.2m (앙카 D16 @0.3m, L=0.2m, 거푸집 편측)

NO.1
맨홀(D600) 숭상 1EA

1공구 [NOTE]

2026년 건설사업 합동설계반


事業名	年月日	圖面名	가상 마을A 마을안길 정비공사		現場實測		圖面作成		檢圖	圖面番戶	一連番戶	이동장 연락처
2026년 건설사업	2026.09.	事項	전 개 도	縮尺 NONE			***			A -		

가상 마을A 마을안길 정비공사
아스콘 덧씌우기 전개도

(2/2) S = NONE

(2 공 구) L=10.0m

OO면 OO리 OO번지 일원

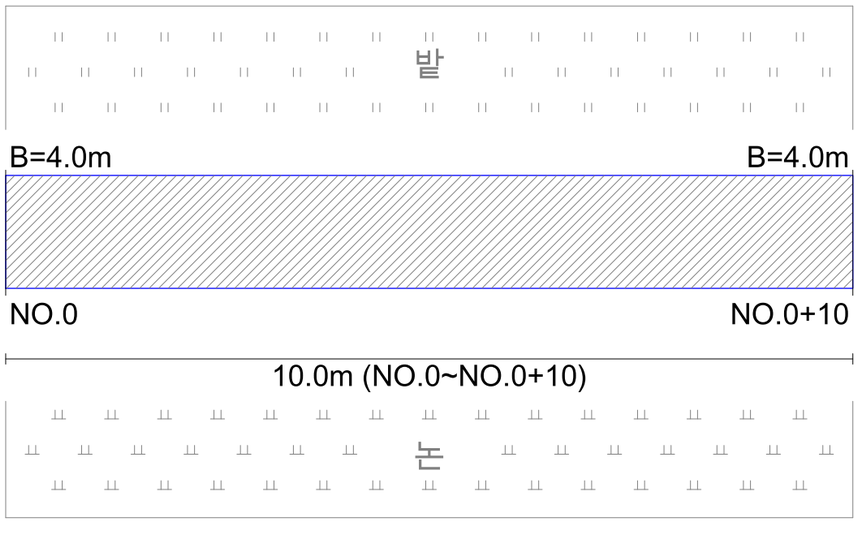

아스콘 덧씌우기

[범 례]

차선도색 없음

NO.0~NO.0+10
아스콘 덧씌우기 L=10.0m, B=4.0m

2공구 [NOTE]

2026년 건설사업 합동설계반

事業名	年月日	圖面名	가상 마을A 마을안길 정비공사			現場實測		圖面作成		檢圖	圖面番戶	一連番戶	이동장 연락처
2026년 건설사업	2026.09.	事項	전 개 도	縮尺	NONE			* * *			A -		