가상 마을E 소하천 호안 정비공사

설 계 도

2026. 10

O O 시

가상 마을E 소하천 호안 정비공사
위　치　도



OO면 OO리 OO번지 지내　식생블럭 L=24.0m, H=2.0m

2026년 건설사업 합동설계반

事業名	年月日	圖面名	가상 마을E 소하천 호안 정비공사		現場實測		圖面作成		檢圖	圖面番戶	一連番戶	이동장 연락처
2026년 건설사업	2026.10.	事項	위 치 도	縮尺 NONE			* * *			A -		


가상 마을E 소하천 호안 정비공사
평 면 도 · 정 면 도

평면 S = 1:200 · 정면 S = 가로 1:200, 세로 1:100


(호 안 공) L=24.0m H=2.0m (4단)

OO면 OO리 OO번지 지내

[평 면 도]

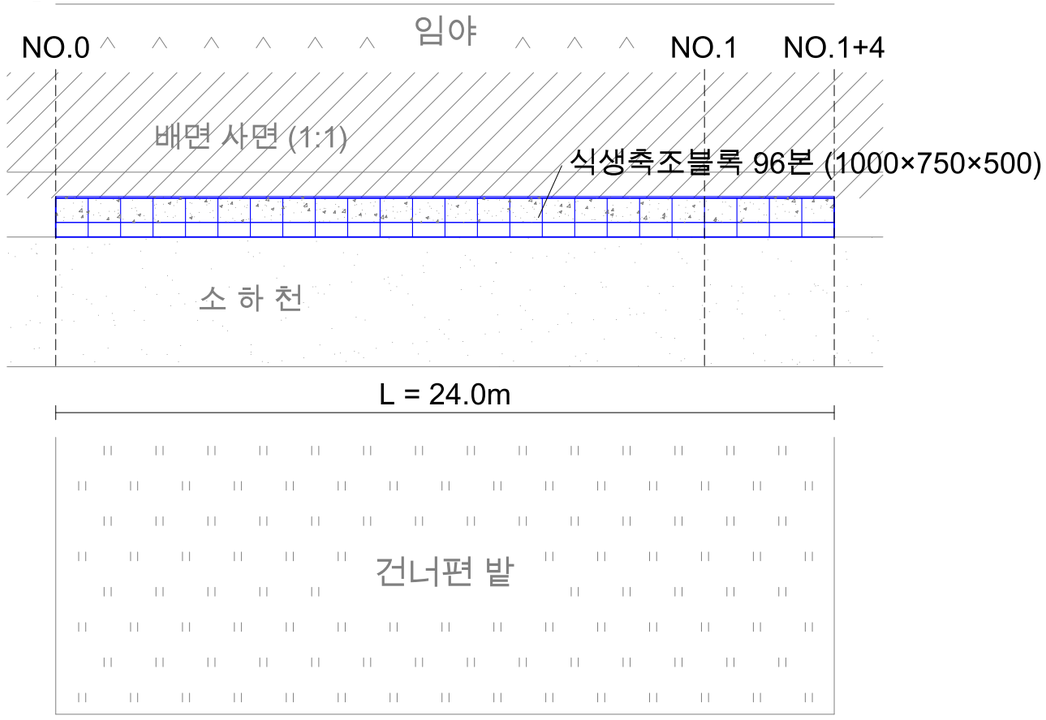

[정 면 도] (전면에서 봄, 세로 2배)

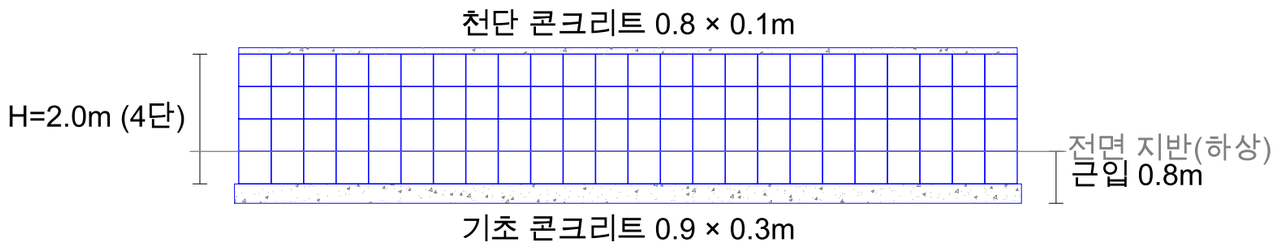

기존 지반·시설 (회색)
터파기선 (1:1)
부직포 (흡출방지)
뒷채움 쇄골재 25mm
기초·천단 콘크리트
식생축조블록 (신설)

[범 례]

식생블럭
식생축조블록 1000×750×500 96본
L=24.0m, H=2.0m (4단, 1단 근입), A=48.0㎡
기초·천단
기초 0.9×0.3m, 천단 0.8×0.1m (25-18-8)
기초 거푸집 합판 6회, 천단 유로폼
뒷채움
쇄골재 25mm (속채움·뒷채움)
부직포 흡출방지 A=50.2㎡
터파기·잔토
기초 바닥 양 끝에서 1:1 (여유 0.5m)
잔토 현장깔기
블럭 형상은 제조사 표준도 기준

[NOTE]

2026년 건설사업 합동설계반

事業名	年月日	圖面名	가상 마을E 소하천 호안 정비공사	現場實測	圖面作成	檢圖	圖面番戶	一連番戶	이동장 연락처
2026년 건설사업	2026.10.	事項	평 면 도	縮尺 1:200	***		A -		


가상 마을E 소하천 호안 정비공사
횡 단 면 도 · 상 세 도

횡단 S = 1:50 · 상세 S = 1:25

(호 안 공) L=24.0m H=2.0m (4단)

OO면 OO리 OO번지 지내

[대표 횡단면도] S=1:50 (NO.0 ~ NO.1+4 같은 단면)

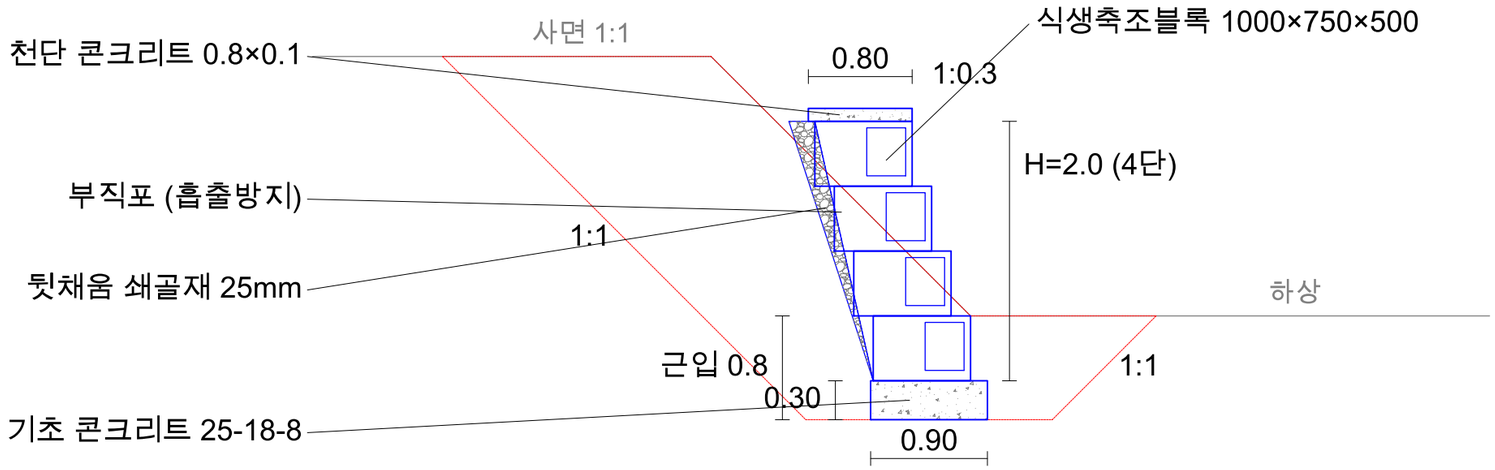


L=24.0 H=2.0m (4단)

[단위수량표] (1m당)

터파기	6.30 ㎡	천단 콘크리트	0.08 ㎥
되메움	5.08 ㎡	속채움 쇄골재	0.24 ㎥
잔토(현장깔기)	1.22 ㎡	뒷채움 쇄골재	0.2 ㎥
블럭 높이	H = 2.0m	부직포	2.09 ㎡
기초 콘크리트	0.27 ㎥	식생블럭	4 본

[블록 상세도] S=1:25

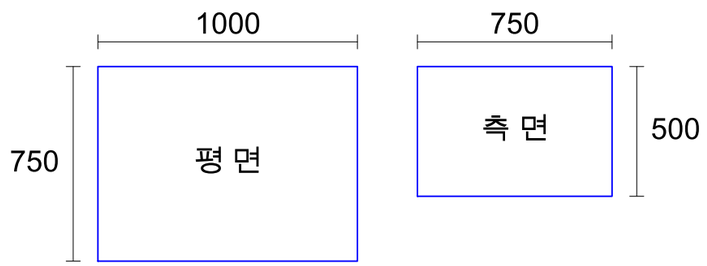

식생축조블록 1000×750×500 (약 390kg)

세부 형상·식재공은 제조사 표준도 참조

기존 지반·시설 (회색)
터파기선 (1:1)
부직포 (흡출방지)
뒷채움 쇄골재 25mm
기초·천단 콘크리트
식생축조블록 (신설)

[범 례]

블럭
4단 쌓기, 단마다 0.15m 물림 (1:0.3)
1단은 전면 지반 아래 근입

기초
0.9×0.3m, 블럭 앞굽 0.13m
기초 바닥 = 전면 지반 −0.8m (근입)

시공 순서
① 터파기 ② 기초 타설
④ 양생 ⑤ 블럭 쌓기·부직포·뒷채움·속채움
⑥ 천단 ⑦ 되메움

안정 검토(간이, φ30°)
활동 1.31 · 전도 2.11 · 편심 0.07m (B/6 0.15)
시행쐐기(φ30°, δ=2/3φ, c=0, 상재 0, 활동면 ≥ 사면각 45.0°)
기준 KDS 11 80 25:2024(활동 1.5 · 전도 1.5)

안정 검토(간이, φ35°)
활동 2.10 · 전도 2.81 · 편심 -0.01m (B/6 0.15)
시행쐐기(φ35°, δ=2/3φ, c=0, 상재 0, 활동면 ≥ 사면각 45.0°)
기준 KDS 11 80 25:2024(활동 1.5 · 전도 1.5)

터파기 후 배면 지반 확인, 연약 시 하단 보강(설계변경)

[NOTE]