


가상 마을B 마을안길 정비공사

설 계 도

2026. 09

○ ○ 시

가상 마을B 마을안길 정비공사 위 치 도

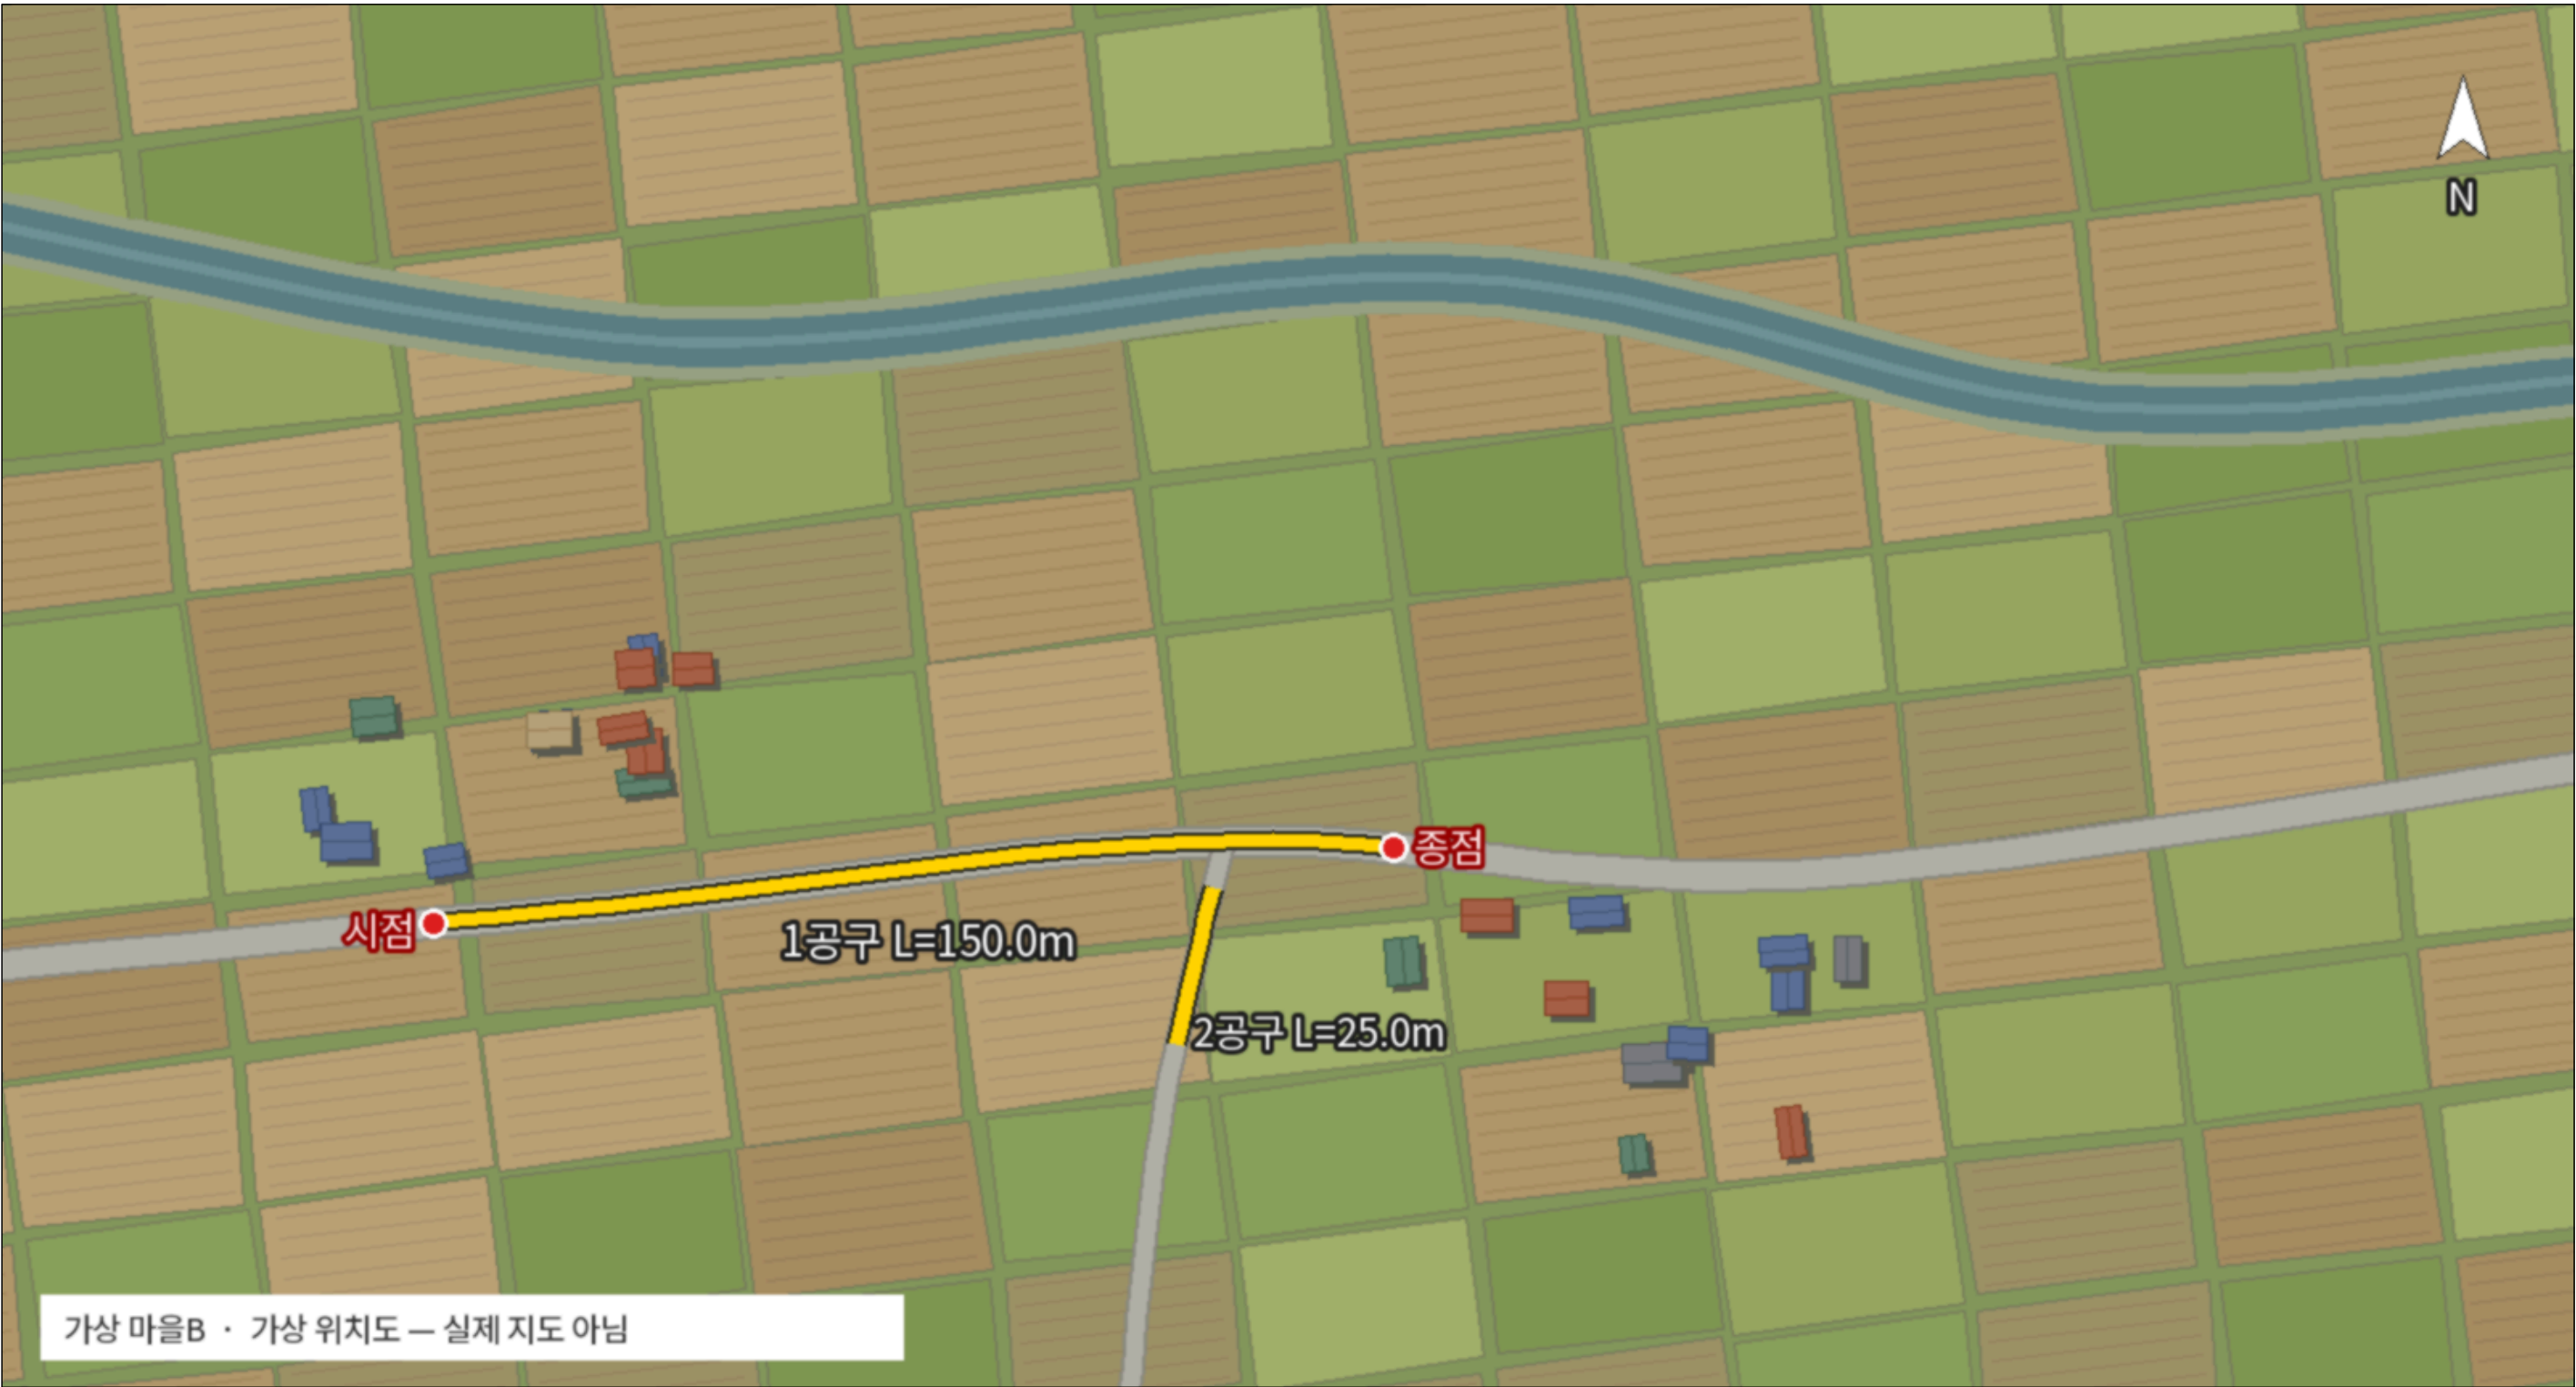


(1공구) 00면 00리 00번지 일원 L=150.0m
(2공구) 00면 00리 00번지 일원 L=25.0m

가상 마을B 마을안길 정비공사
아스콘 덧씌우기 전개도

(1/2) S = NONE

(1 공 구) L=150.0m 00면 00리 00번지 일원

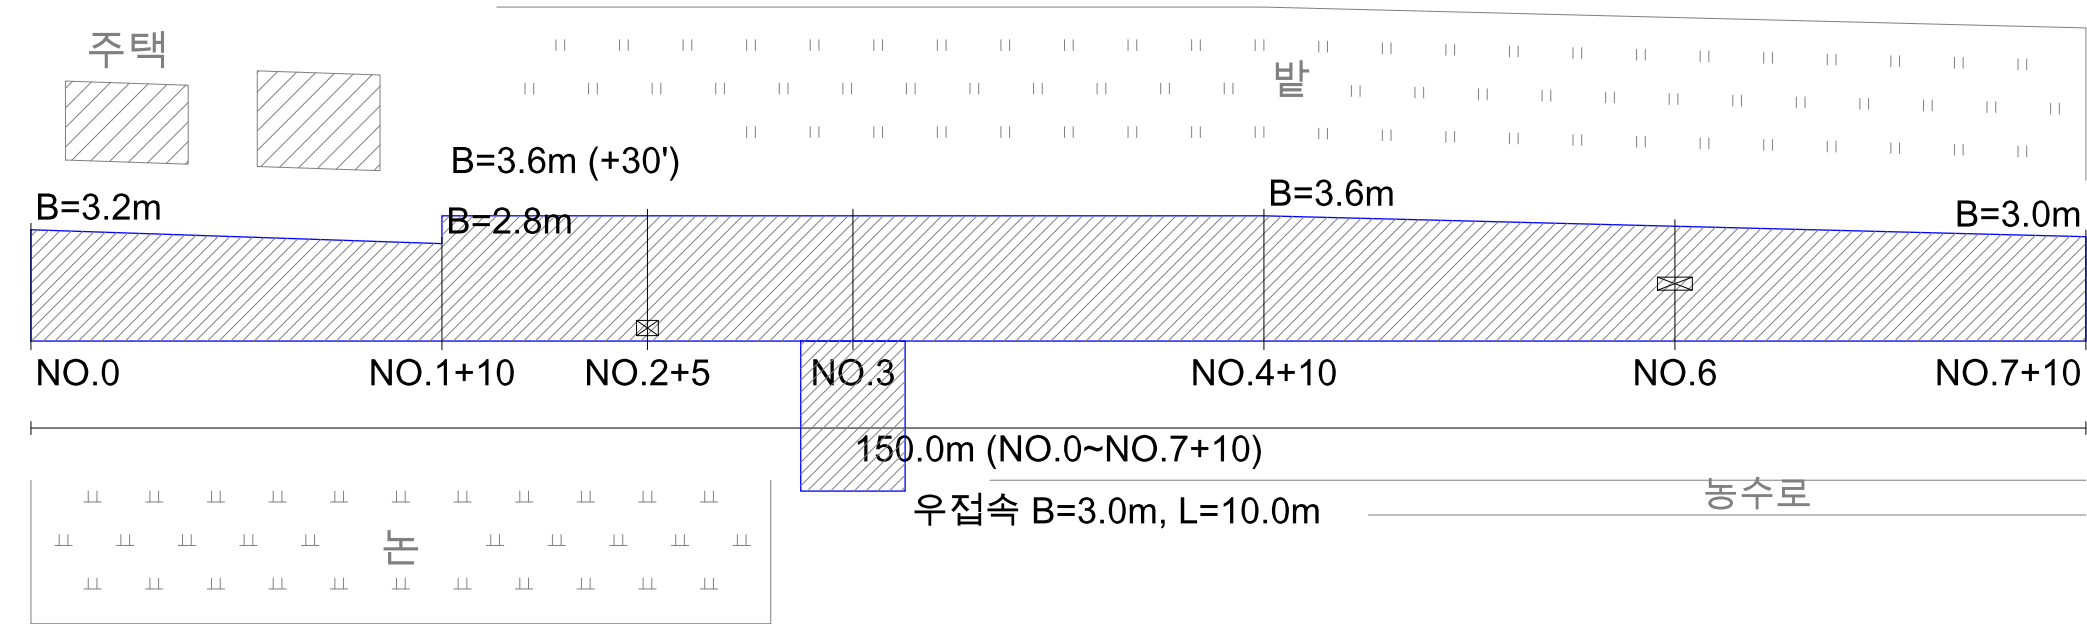

☒ 집수정 승상 (1000×1000·2000×500)

▨ 아스콘 덧씌우기

[범 례]

NO.0~NO.7+10
차선도색(백색실선) 양측 L=317.0m

NO.6
집수정(2000×500) 승상 1EA

NO.3
우접속 아스콘 B=3.0m, L=10.0m


NO.2+5
집수정(1000×1000) 승상 1EA

1공구 [NOTE]

가상 마을B 마을안길 정비공사
아스콘 덧씌우기 전개도

(2/2) S = NONE

(2 공 구) L=25.0m 00면 00리 00번지 일원

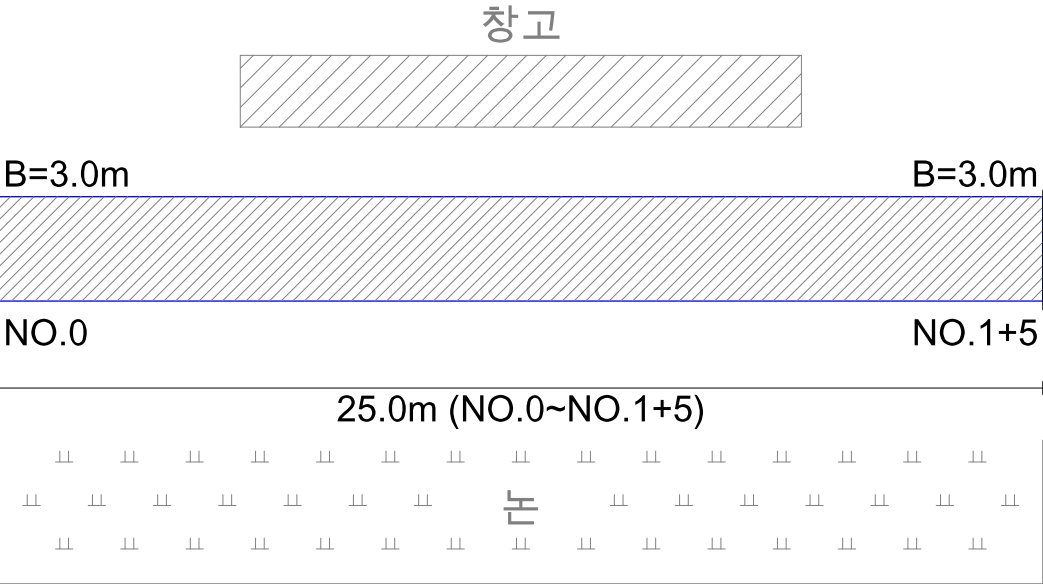

아스콘 덧씌우기
[범 례]
NO.0~NO.1+5
차선도색(백색실선) 양측 L=50.0m
NO.0~NO.1+5
아스콘 덧씌우기 L=25.0m, B=3.0m
2공구 [NOTE]

事 業 名	年 月 日	圖 面 名	가상 마을B 마을안길 정비공사	現 場 實 測	圖 面 作 成	檢 圖	圖面番戶	一連番戶	이동장 연락처
2026년 건설사업	2026.09.	事 項	전 개 도	縮 尺	NONE		A -		