

가상 마을D 배수로 정비공사
설 계 도

2026. 10

○ ○ 시


가상 마을D 배수로 정비공사 위 치 도



(1공구) 00면 00리 00번지 일원 L=128.1m

(1/3) S = 1:400 (A3)

00면 00리 00번지 일원

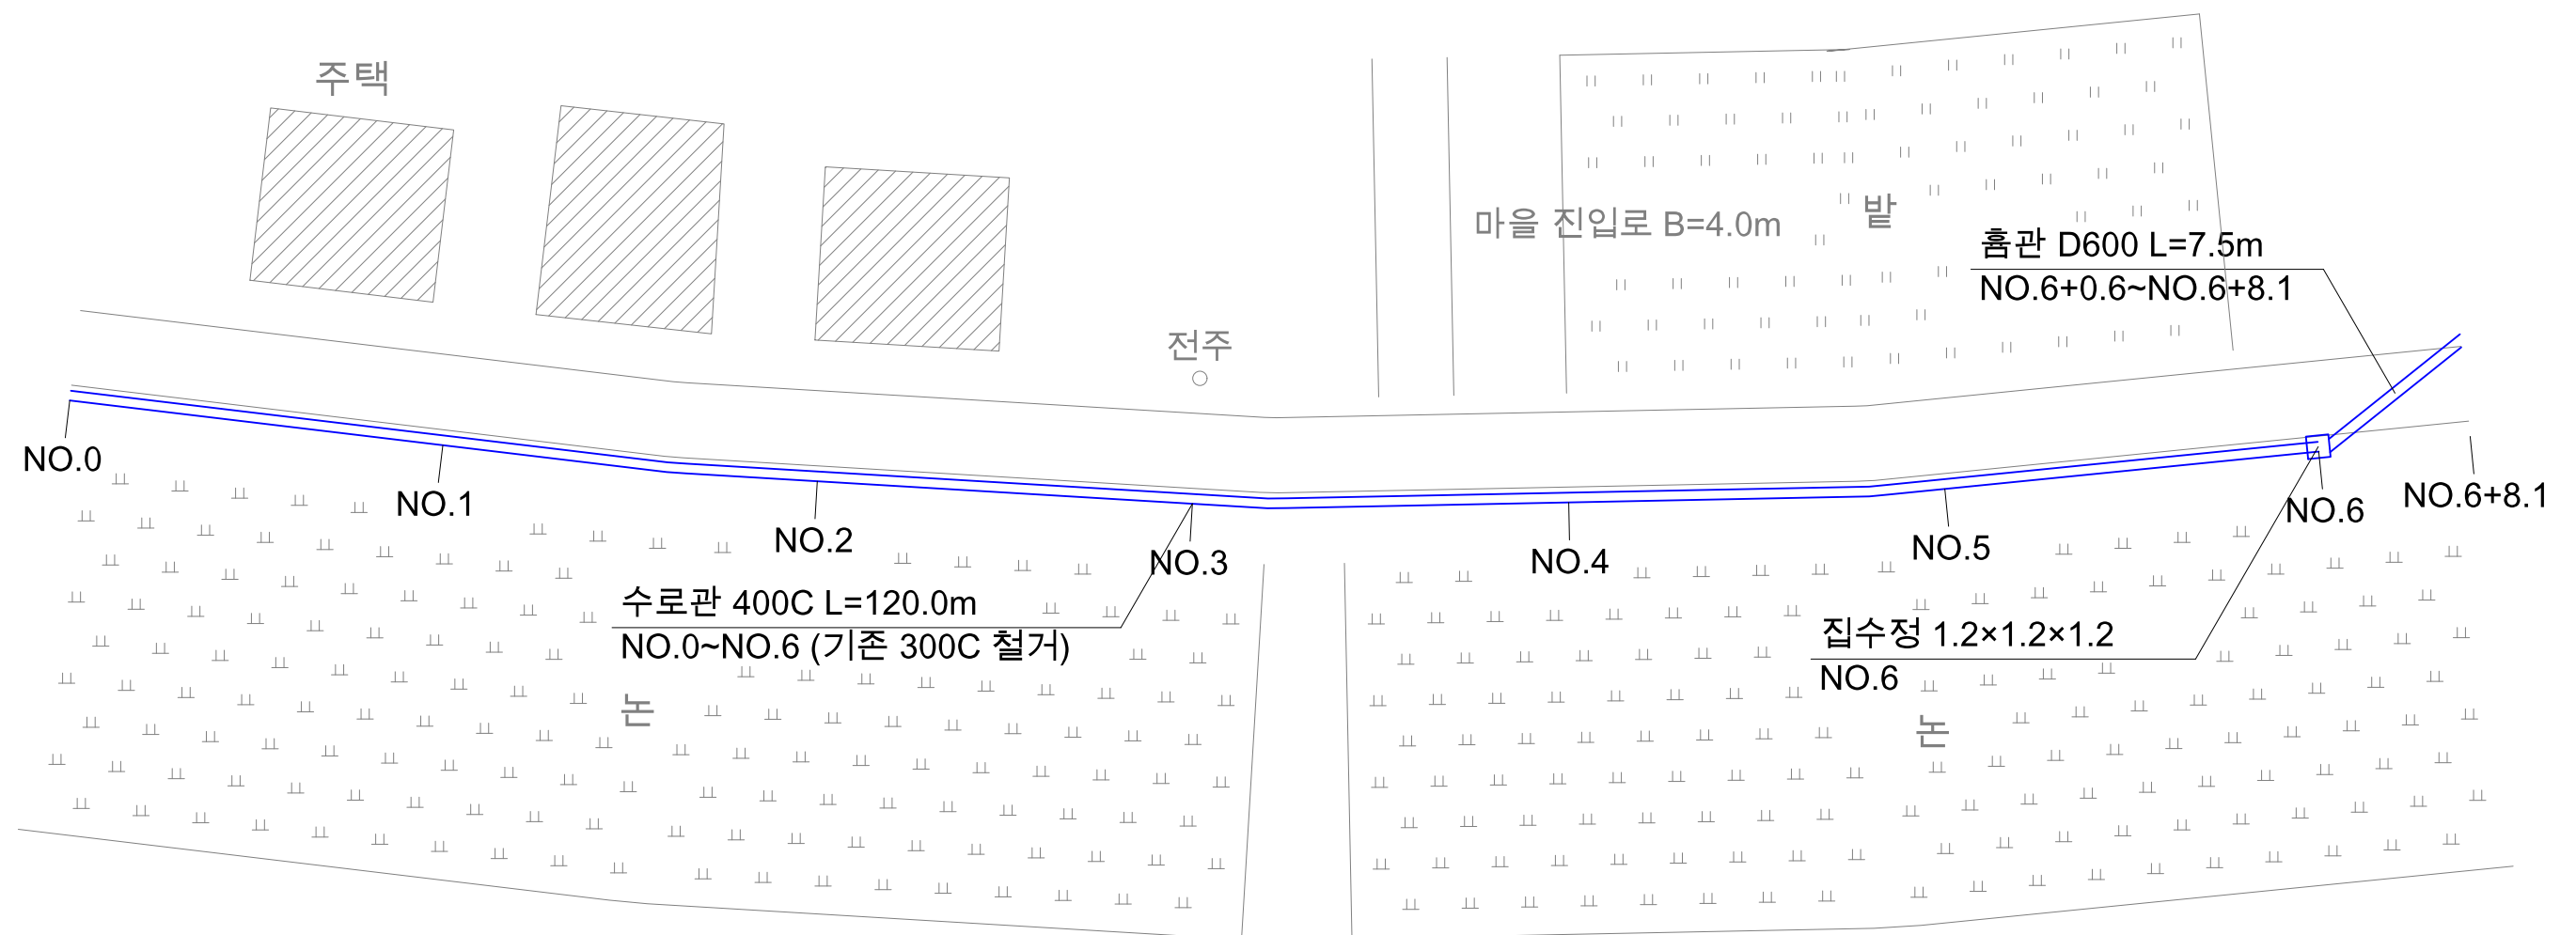

2026년 건설사업 합동설계반













事 業 名	年 月 日	圖 面 名	가상 마을D 배수로 정비공사			現 場 實 測		圖 面 作 成		檢 圖	圖面番戶	一連番戶	이동장 연락처
2026년 건설사업	2026.10.	事 項	계 획 평 면 도	縮 尺	1:400			***			A -		

가상 마을D 배수로 정비공사 횡단면도

(2/3) S = 1:50 (A3)

(1 공 구) L=128.1m 00면 00리 00번지 일원

※ 단위 m · 지반선은 야장(상대 깊이) · 같은 단면 측점은 비고에 생략 표기

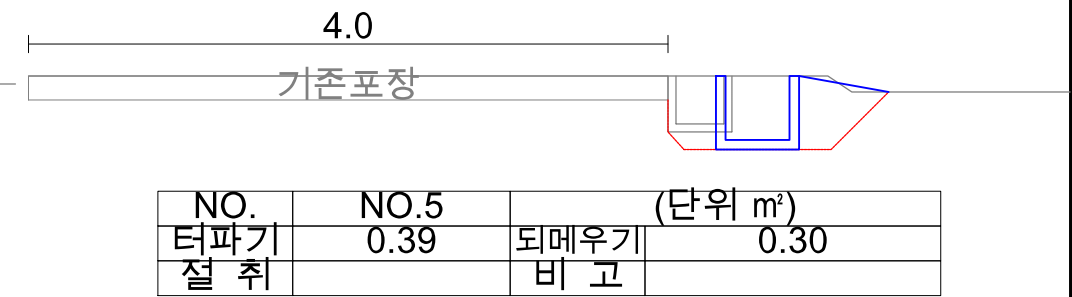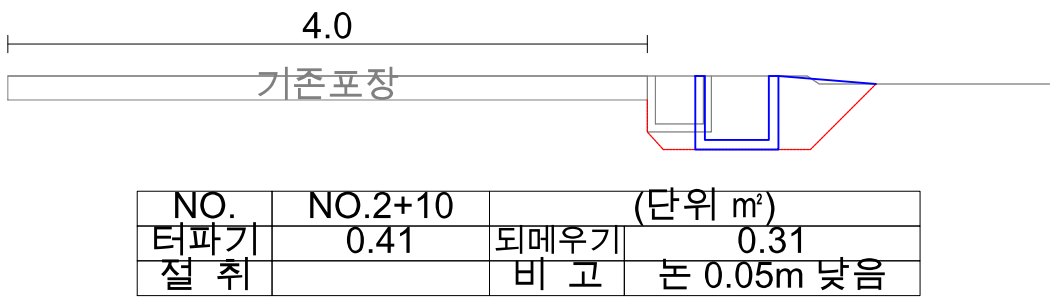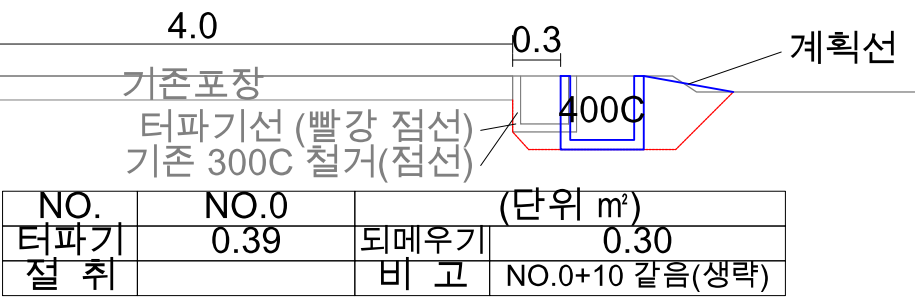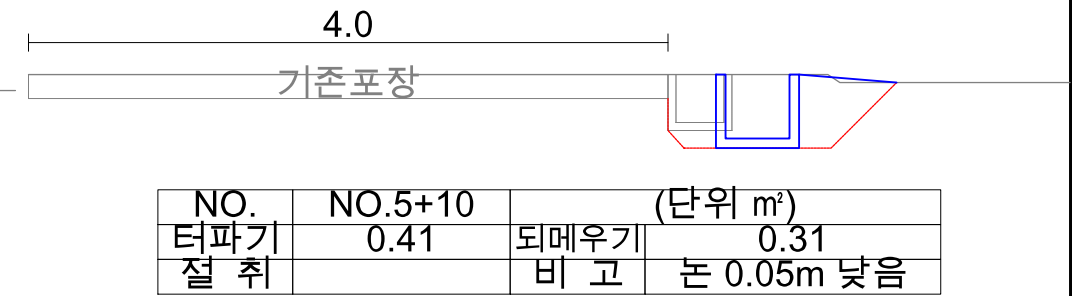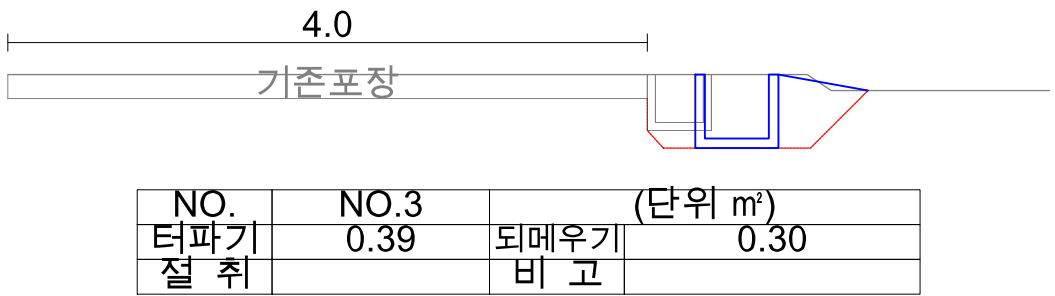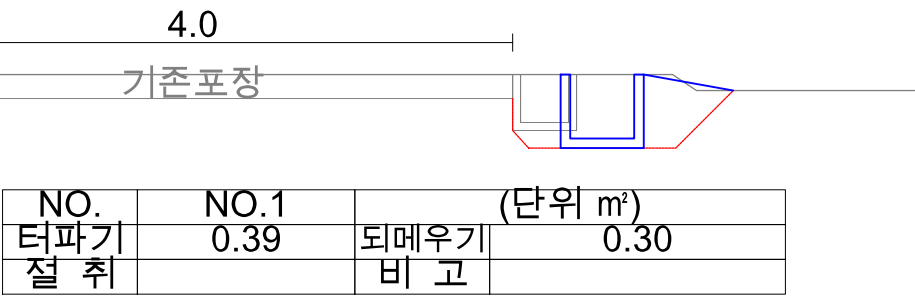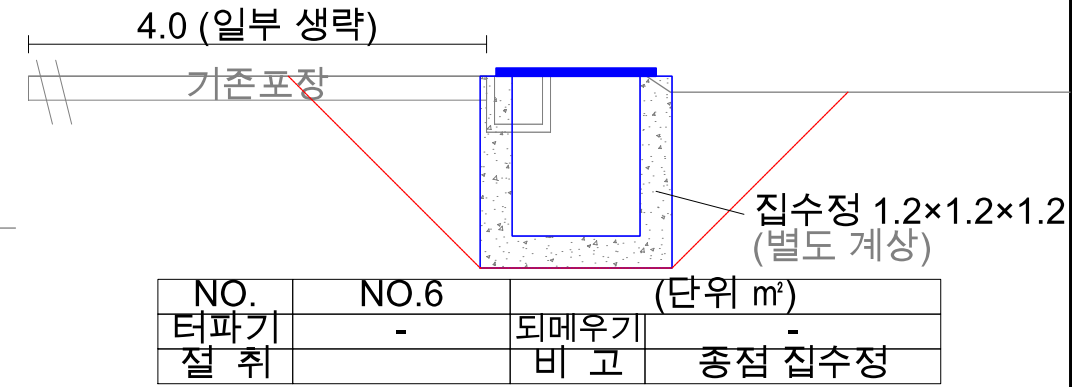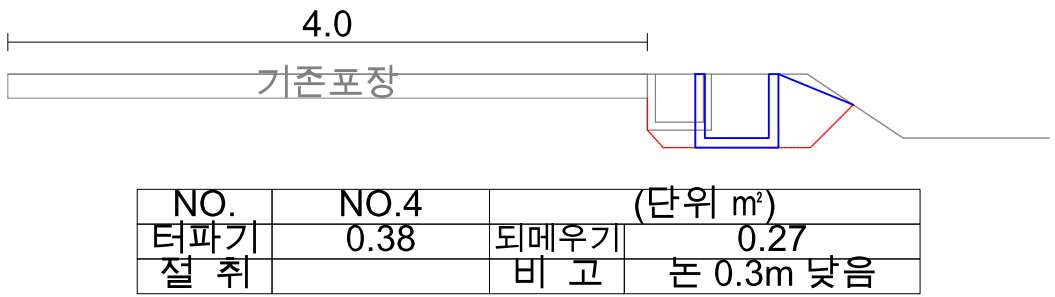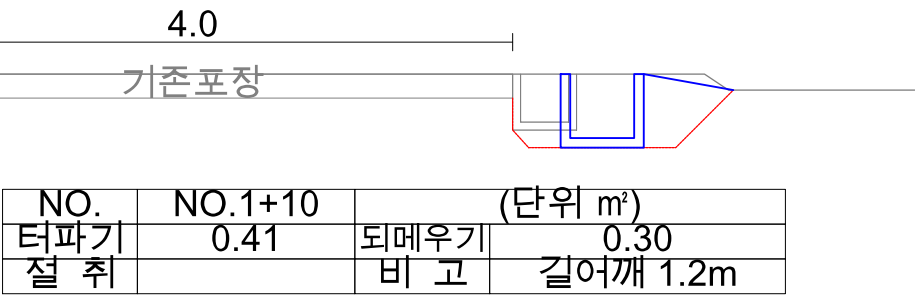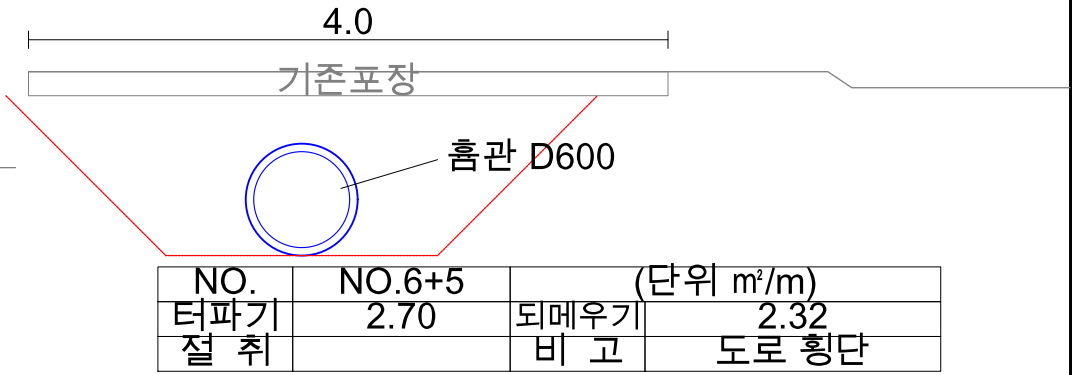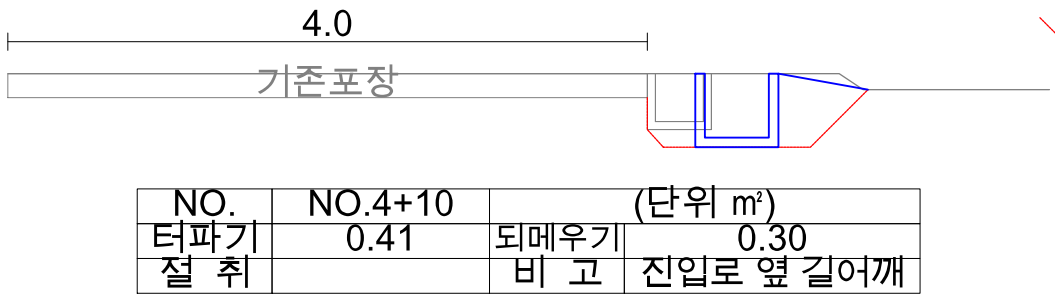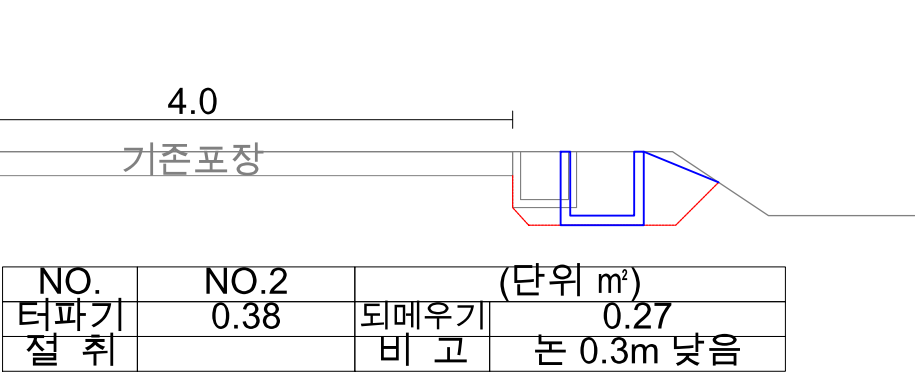

2026년 건설사업 합동설계반


事業名	年月日	圖面名	現場實測	圖面作成	檢圖	圖面番戶	一連番戶	이동장 연락처
2026년 건설사업	2026.10.	事項	가상 마을D 배수로 정비공사	***		A -		
			횡단면도	縮尺 1:50				

가상 마을D 배수로 정비공사
상세도


(3/3) S = 1:20 (A3)

상세도


U형 수로관 400C

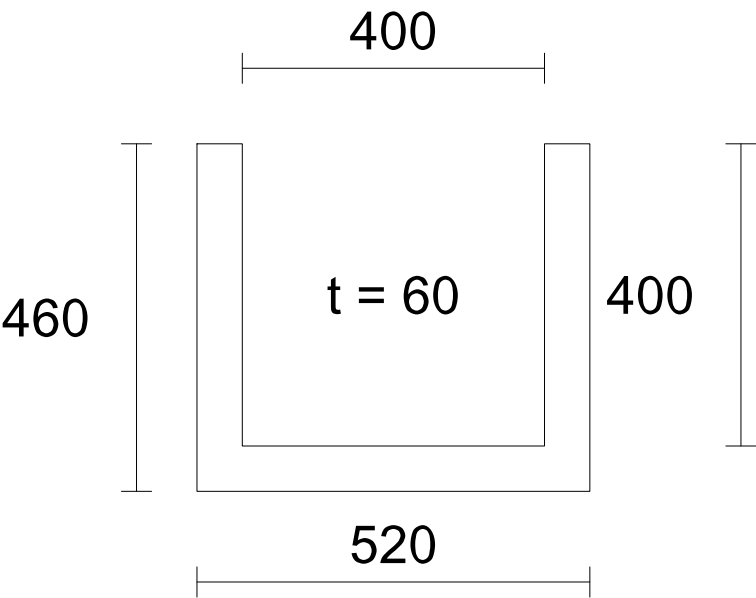

흙관 D600 (고무링 접합)

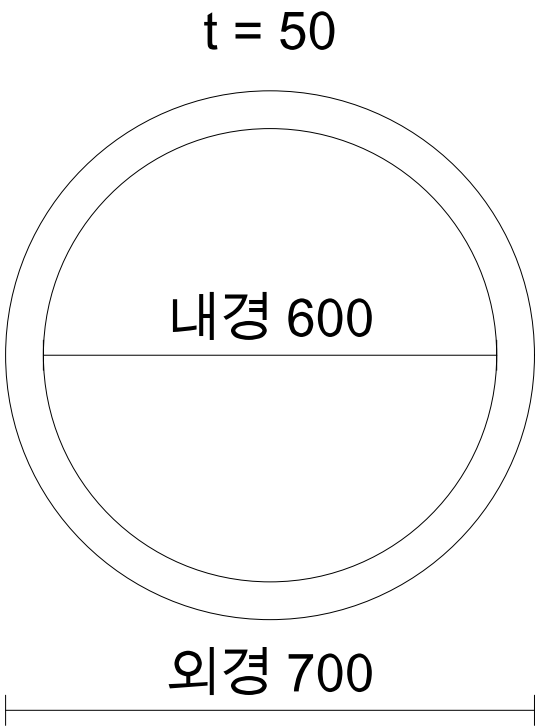

집수정 (단면)

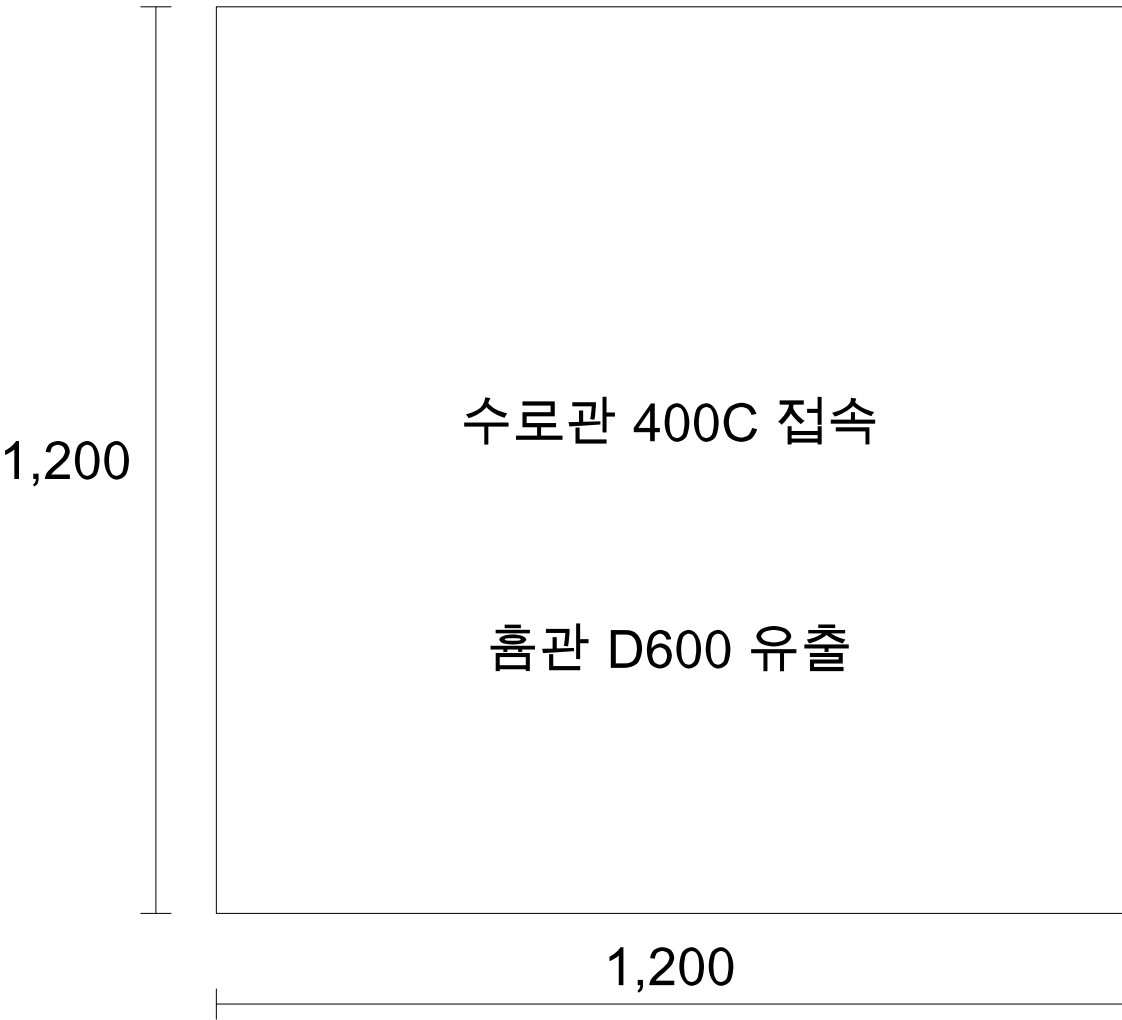

※ 치수 단위 mm — 가상 예제(제품 규격 치수)