

가상 마을C 농로 정비공사

설 계 도

2026. 10

〇 〇 시

가상 마을C 농로 정비공사 위 치 도


(1공구) OO면 OO리 OO번지 일원 콘크리트깨기및복구 B=4.0m, L=42.0m

事 業 名	年 月 日	圖 面 名	가상 마을C 농로 정비공사			現 場 實 測	圖 面 作 成		檢 圖	圖面番戶	一連番戶	이동장 연락처
2026년 건설사업	2026.10.	事 項	위 치 도	縮 尺	NONE			***		A -		

가상 마을C 농로 정비공사
콘크리트깨기및복구 평면도

(1/2) S = NONE

(1 공 구) L=42.0m 00면 00리 00번지 일원

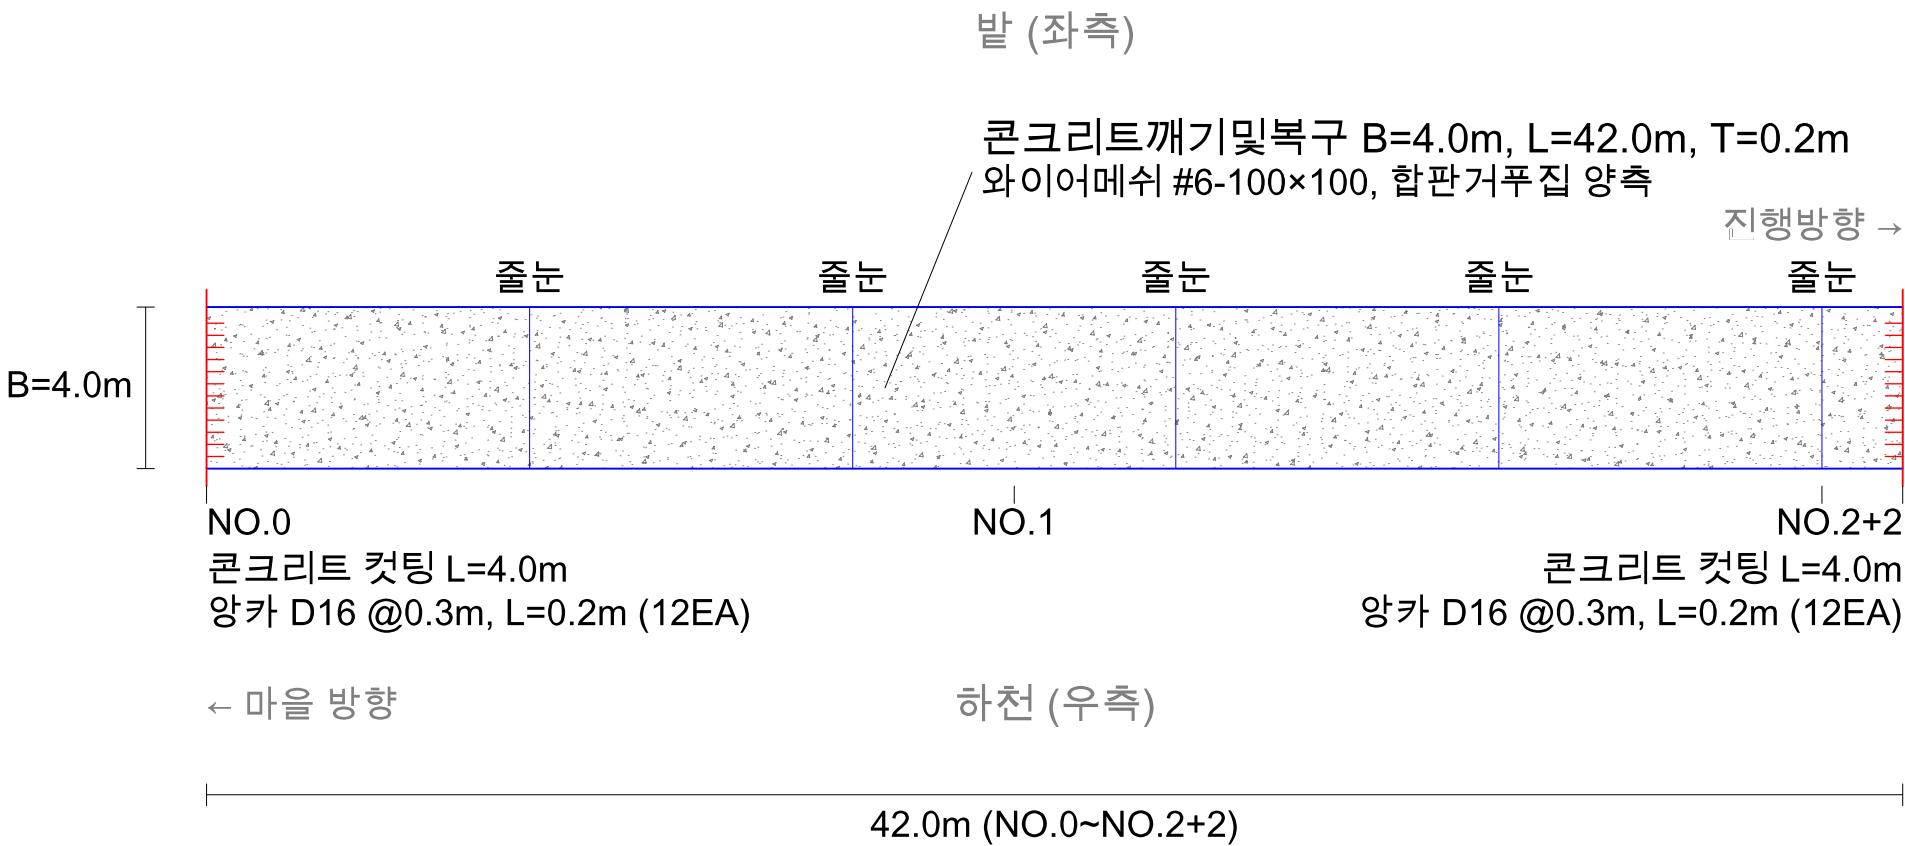

- 콘크리트깨기및복구 (T=0.2m)
- 콘크리트 커팅
- 앙카 D16 @0.3m
- 합판거푸집 (6회)
- 줄눈 @8.0m (종점부 2.0m)

[범 례]

NO.0~NO.2+2
콘크리트깨기및복구 B=4.0m, L=42.0m, T=0.2m
NO.0, NO.2+2
콘크리트 커팅 L=4.0m (2개소)
NO.0, NO.2+2
앙카 D16 @0.3m, L=0.2m
NO.0~NO.2+2
합판거푸집 양측, 줄눈 @8.0m (종점부 2.0m)
NO.0~NO.2+2
와이어메쉬 #6-100x100

1공구 [NOTE]


事業名	年月日	圖面名	現場實測	圖面作成	檢圖	圖面番戶	一連番戶	이동장 연락처
2026년 건설사업	2026.10.	事項 평면도	縮尺 NONE	***		A -		

가상 마을C 농로 정비공사 횡단면도 및 포장 상세도


(2/2) S = NONE

(1 공 구) L=42.0m 00면 00리 00번지 일원


콘크리트포장 표준단면

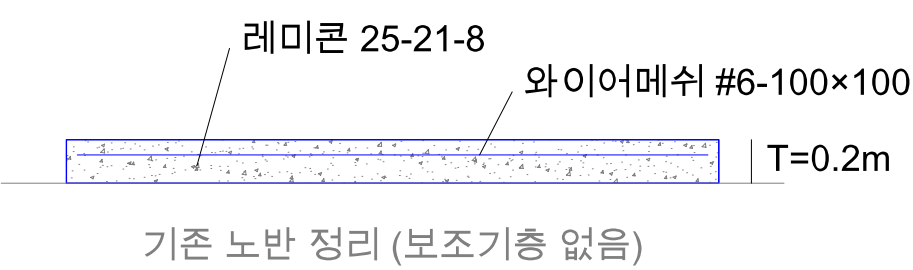

접속부 상세 (NO.0, NO.2+2)

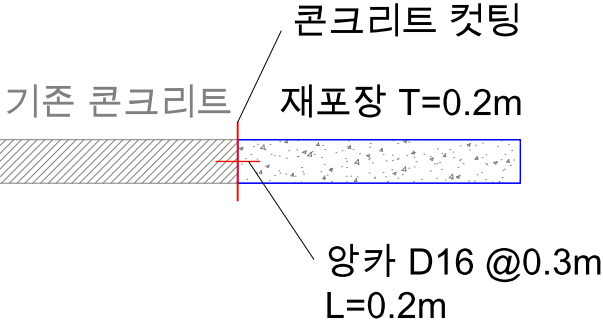

대표 횡단면 (NO.0 ~ NO.2+2)

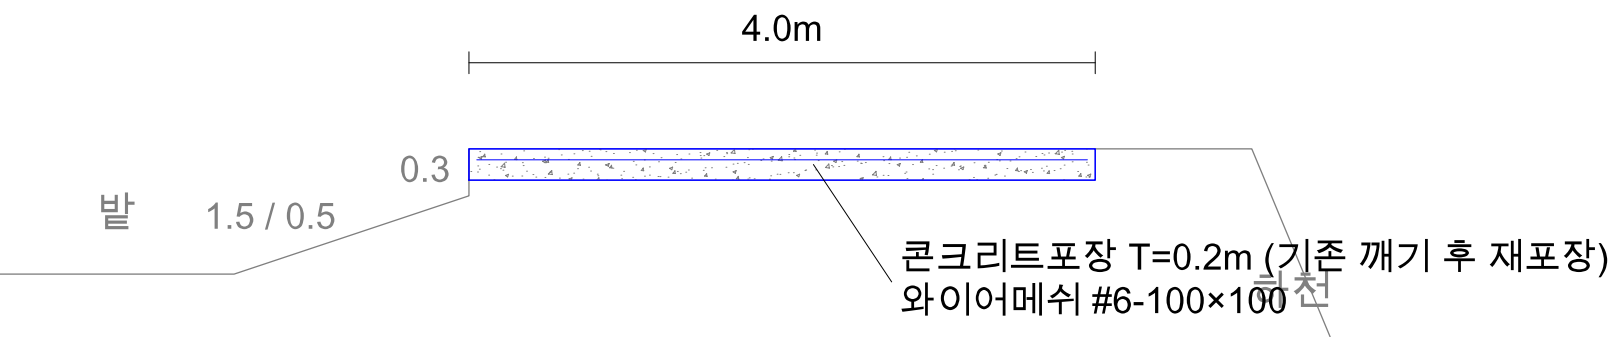

단위면적표 (㎡/m)

절 취		되메움	
성 토		보조기층	
터파기		포장복구	0.80
콘크리트깨기	0.80	잔 토	

NO.0~NO.2+2
기존 콘크리트포장 깨기 T=0.2m
NO.0~NO.2+2
콘크리트포장 B=4.0m, T=0.2m
좌측: 발 (단차 0.3m, 사면 1.5/0.5)
우측: 하천 (사면 0.5/1.2)
1공구 [NOTE]