

가상 마을D 배수로 정비공사
설 계 도

2026. 10

〇 〇 시

가상 마을D 배수로 정비공사 위 치 도


(1공구) L=68.1m
OO면 OO리 OO번지 일원

事 業 名	年 月 日	圖 面 名			現 場 實 測		圖 面 作 成		檢 圖	圖面番戶	一連番戶	이동장 연락처
		事 項	위 치 도	縮 尺	NONE		***			A -		

가상 마을D 배수로 정비공사 계획평면도

(1/3) S = 1:250 (A3)

(1 공 구) L=68.1m 00면 00리 00번지 일원

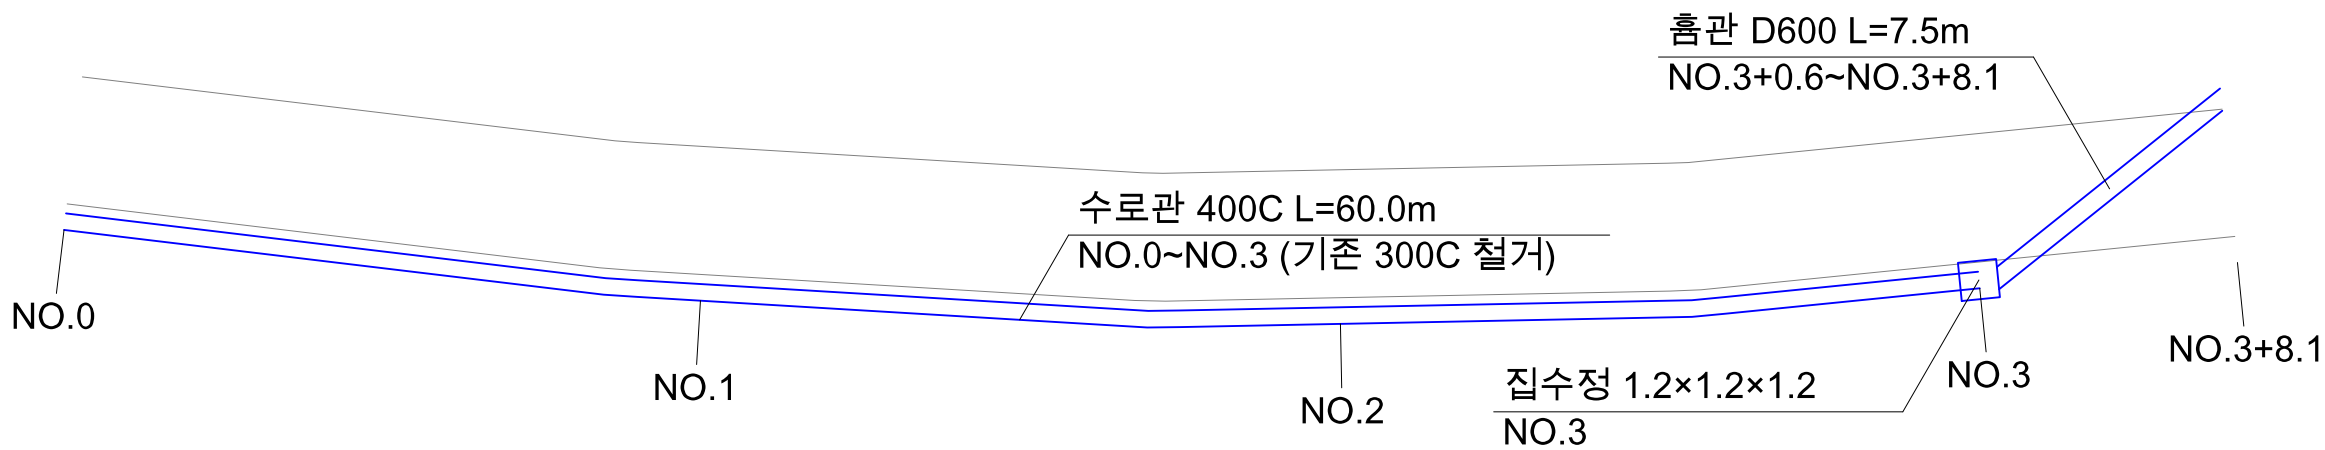


가상 마을D 배수로 정비공사 횡단면도

(2/3) S = 1:50 (A3)


(1 공 구) L=68.1m

00면 00리 00번지 일원


※ 단위 m · 지반선은 야장(상대 깊이) · 같은 단면 측점은 비고에 생략 표기

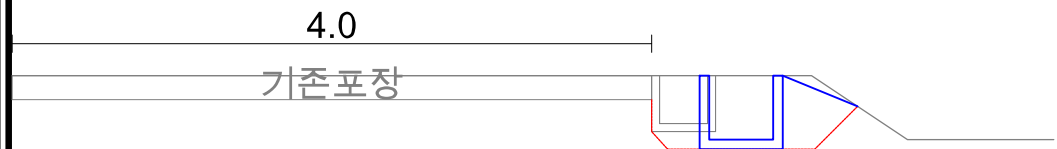


NO.	NO.2	(단위 m²)	
터파기	0.38	되메우기	0.27
절 취		비 고	논 0.3m 낮음

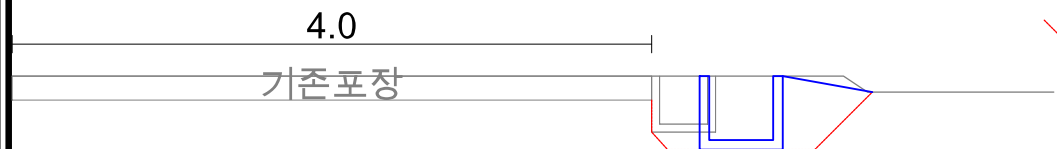


NO.	NO.1+10	(단위 m²)	
터파기	0.41	되메우기	0.30
절 취		비 고	길어깨 1.2m

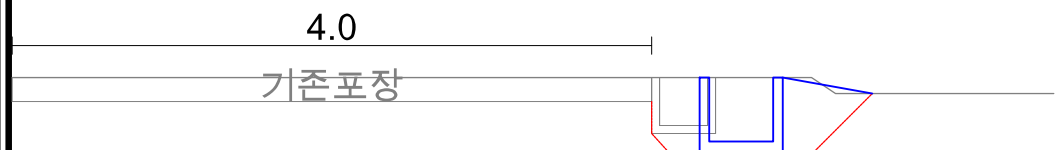


NO.	NO.1	(단위 m²)	
터파기	0.39	되메우기	0.30
절 취		비 고	

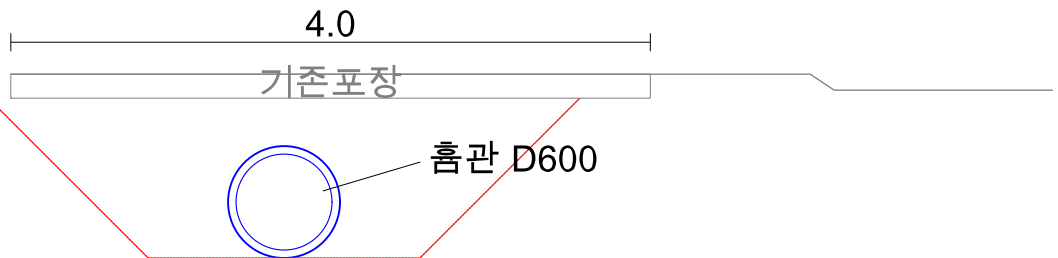


NO.	NO.3+5	(단위 m²/m)	
터파기	2.70	되메우기	2.32
절 취		비 고	도로 횡단

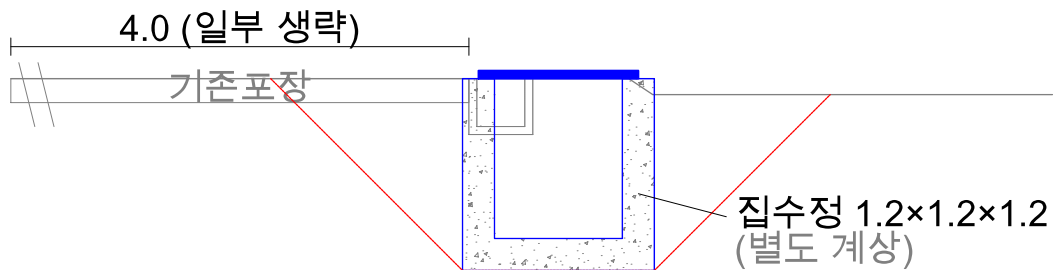

NO.	NO.3	(단위 m²)	
터파기	-	되메우기	-
절 취		비 고	종점 집수정

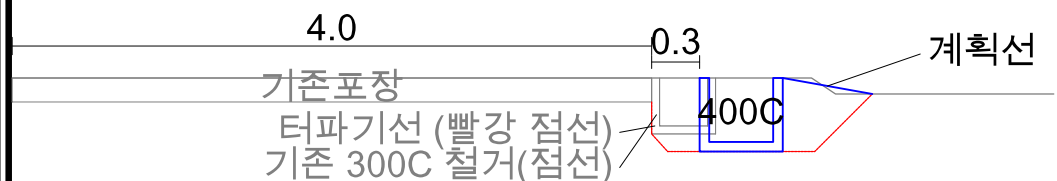

NO.	NO.0	(단위 m²)	
터파기	0.39	되메우기	0.30
절 취		비 고	NO.0+10 같음(생략)

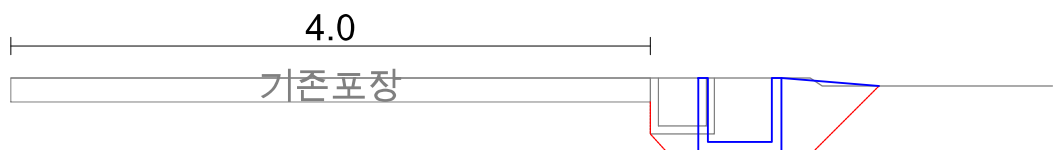

NO.	NO.2+10	(단위 m²)	
터파기	0.41	되메우기	0.31
절 취		비 고	논 0.05m 낮음

2026년 건설사업 합동설계반


事業名	年月日	圖面名	現場實測	圖面作成	檢圖	圖面番戶	一連番戶	이동장 연락처
2026년 건설사업	2026.10.	事項 가상 마을D 배수로 정비공사 횡 단 면 도	縮 尺 1:50	***		A -		

가상 마을D 배수로 정비공사
상세도


(3/3) S = 1:20 (A3)

상세도

U형 수로관 400C

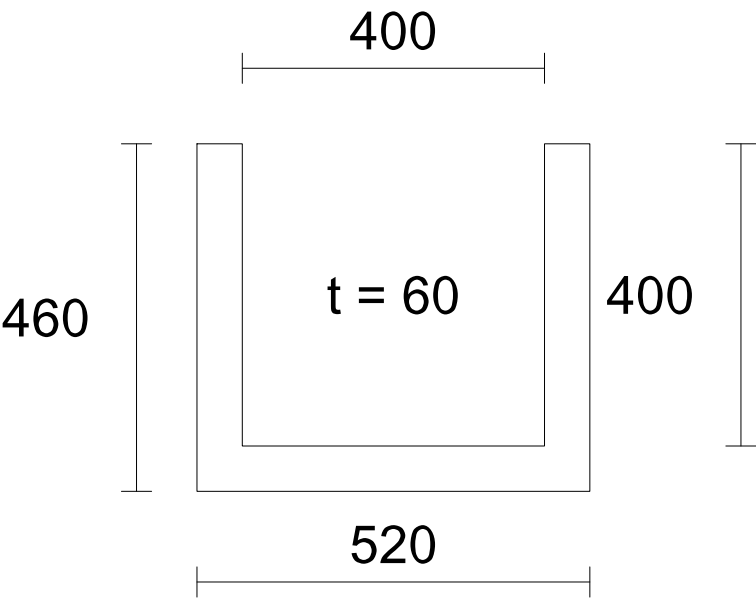

흙관 D600 (고무링 접합)

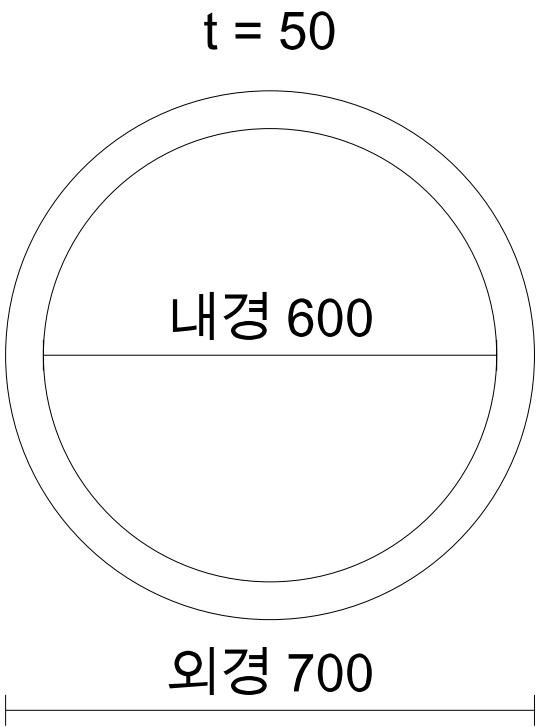

집수정 (단면)



※ 치수 단위 mm — 가상 예제(제품 규격 치수)