

가상 마을E 소하천 호안 정비공사

설 계 도

2026. 10

〇 〇 시

가상 마을E 소하천 호안 정비공사
위 치 도

OO면 OO리 OO번지 지내 식생블럭 L=24.0m, H=2.0m

事 業 名	年 月 日	圖 面 名	가상 마을E 소하천 호안 정비공사			現 場 實 測	圖 面 作 成		檢 圖	圖面番戶	一連番戶	이동장 연락처
2026년 건설사업	2026.10.	事 項	위 치 도	縮 尺	NONE			***		A -		


가상 마을E 소하천 호안 정비공사 평면도 · 정면도

평면 S = 1:200 · 정면 S = 가로 1:200, 세로 1:100


(호 안 공) L=24.0m H=2.0m (4단)

00면 00리 00번지 지내

[평면도]

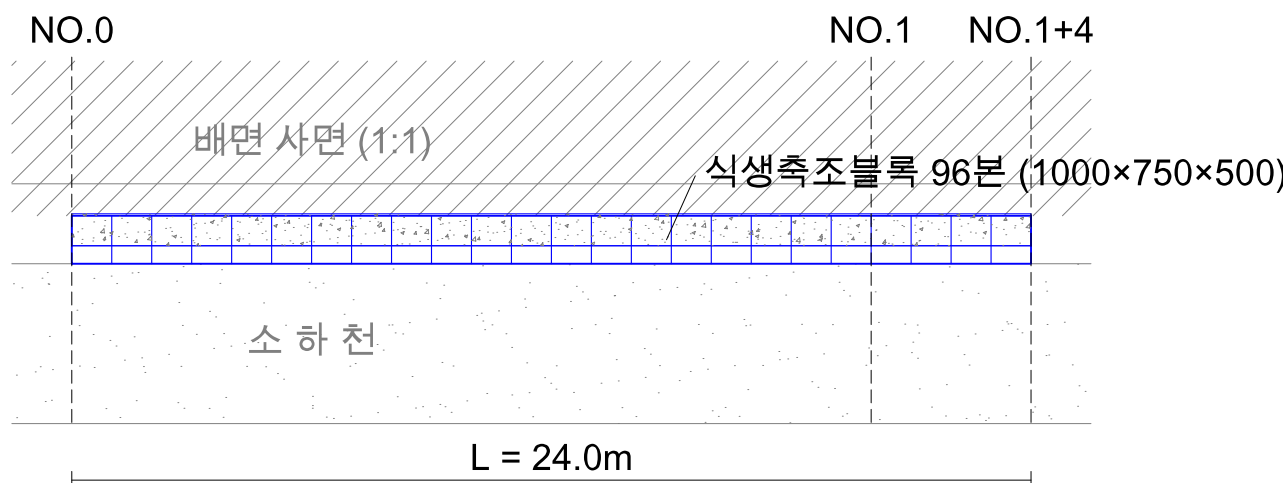

[정면도] (전면에서 봄, 세로 2배)

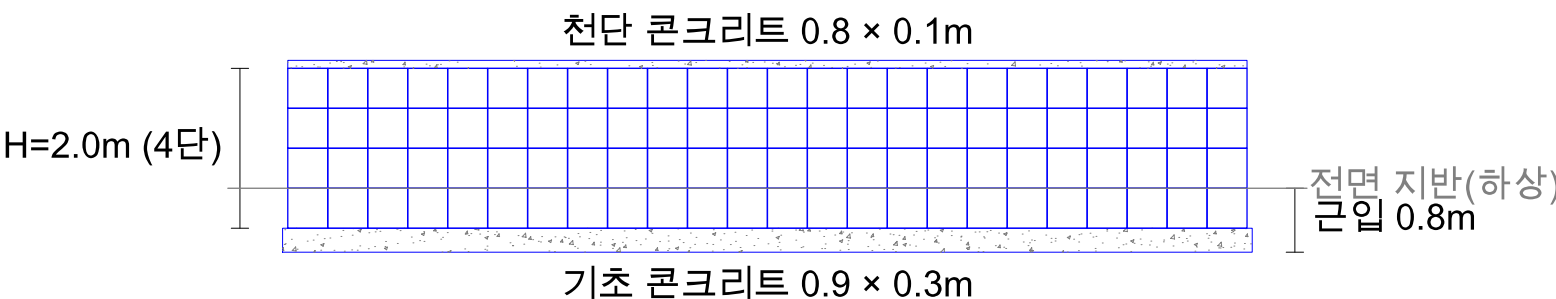

- 기존 지반·시설 (회색)
- 터파기선 (1:1)
- 부직포 (흡출방지)
- 식생축조블록 1000x750x500 96본
- 기초·천단 콘크리트
- 식생축조블록 (신설)

[범례]

식생블럭
식생축조블록 1000x750x500 96본
L=24.0m, H=2.0m (4단, 1단 근입), A=48.0m²
기초·천단
기초 0.9x0.3m, 천단 0.8x0.1m (25-18-8)
기초 거푸집 합판 6회, 천단 유로폼
틈채움
쇄골재 25mm (속채움·틈채움)
부직포 흡출방지 A=50.2m²
터파기·잔토
기초 바닥 양 끝에서 1:1 (여유 0.5m)
잔토 현장갈기
블럭 형상은 제조사 표준도 기준

[NOTE]

2026년 건설사업 합동설계반

事業名	年月日	圖面名	現場實測	圖面作成	檢圖	圖面番戶	一連番戶	이동장 연락처
2026년 건설사업	2026.10.	가상 마을E 소하천 호안 정비공사 평면도	縮尺 1:200	***		A -		


가상 마을E 소하천 호안 정비공사 횡 단 면 도 · 상 세 도

횡단 S = 1:50 · 상세 S = 1:25

(호 안 공) L=24.0m H=2.0m (4단)

00면 00리 00번지 지내

[대표 횡단면도] S=1:50 (NO.0 ~ NO.1+4 같은 단면)

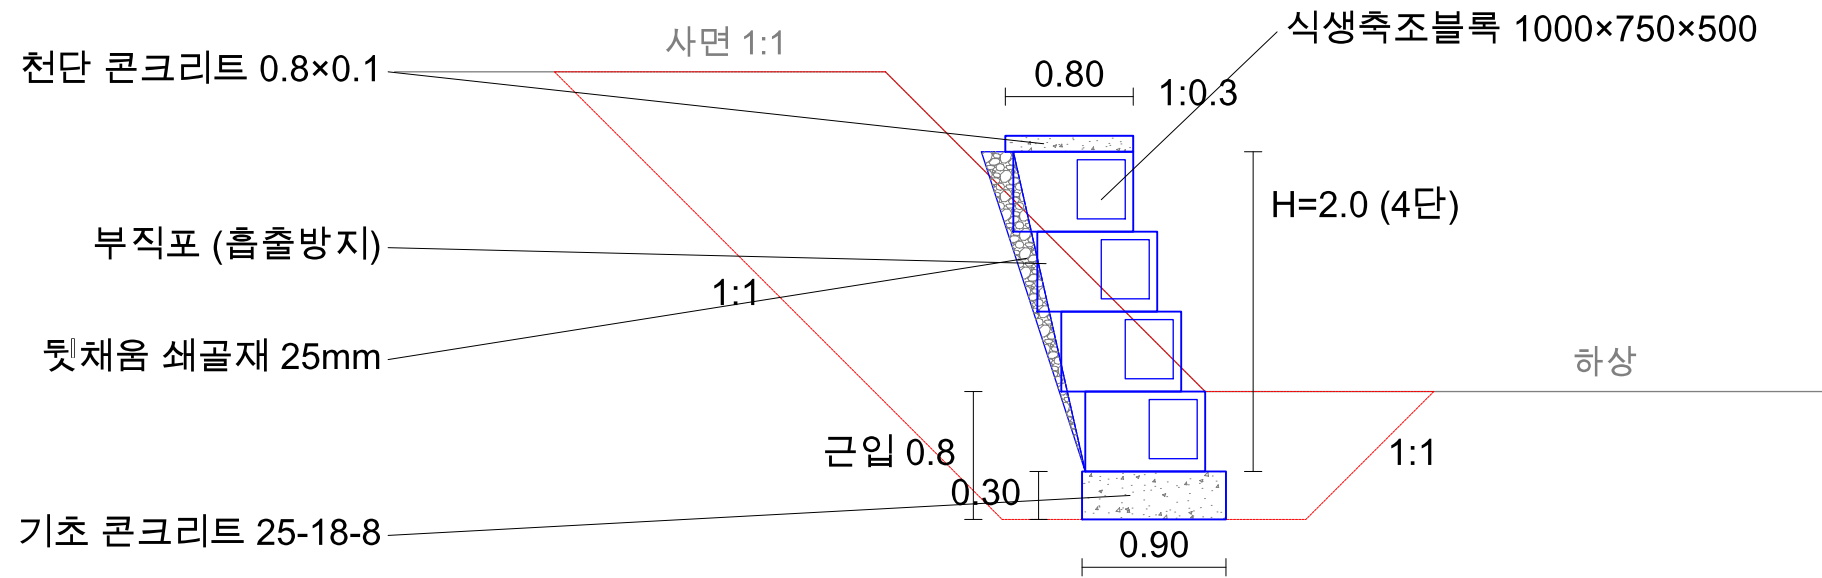


L=24.0 H=2.0m (4단)

[단위수량표] (1m당)

터파기	6.30 m²	천단 콘크리트	0.08 m³
되메움	5.08 m²	속채움 쇠골재	0.24 m³
잔토(현장갈기)	1.22 m²	틔채움 쇠골재	0.2 m³
블럭 높이	H = 2.0m	부직포	2.09 m²
기초 콘크리트	0.27 m³	식생블럭	4 본

[블럭 상세도] S=1:25

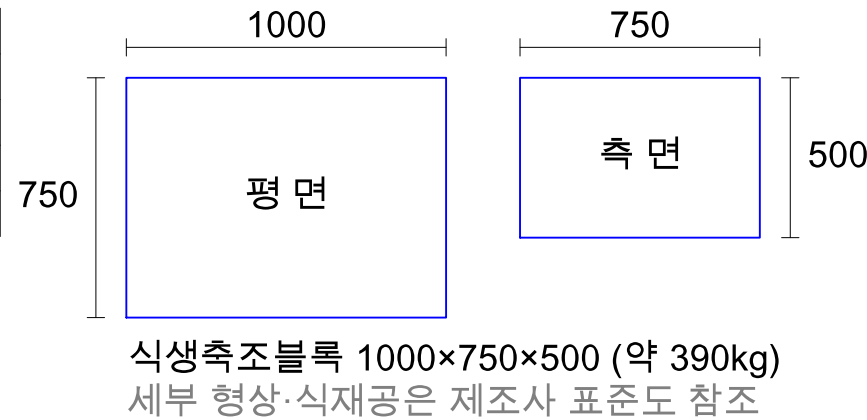

- 기존 지반·시설 (회색)
- 터파기선 (1:1)
- 부직포 (흡출방지)
- ▨ 틔채움 쇠골재 25mm
- ▨ 기초·천단 콘크리트
- 식생축조블럭 (신설)

[범례]

블럭
4단 쌓기, 단마다 0.15m 물림 (1:0.3)
1단은 전면 지반 아래 근입

기초
0.9×0.3m, 블럭 앞굽 0.13m
기초 바닥 = 전면 지반 -0.8m (근입)

시공 순서
① 터파기 ② 기초 타설
④ 양생 ⑤ 블럭 쌓기·부직포·틔채움·속채움
⑥ 천단 ⑦ 되메움

안정 검토(간이, $\phi 30^\circ$)
활동 1.31 · 전도 2.11 · 편심 0.07m (B/6 0.15)
시행빼기($\phi 30^\circ$, $\delta=2/3\phi$, $c=0$, 상재 0, 활동면 $\geq$ 사면각 45.0°)

안정 검토(간이, $\phi 35^\circ$)
활동 2.10 · 전도 2.81 · 편심 -0.01m (B/6 0.15)
시행빼기($\phi 35^\circ$, $\delta=2/3\phi$, $c=0$, 상재 0, 활동면 $\geq$ 사면각 45.0°)

터파기 후 배면 지반 확인, 연약 시 하단 보강(설계변경)

[NOTE]

2026년 건설사업 합동설계반

事業名

年月日

圖面名

가상 마을E 소하천 호안 정비공사

現場實測

圖面作成

檢圖

圖面番戶

一連番戶

이동장 연락처

2026년 건설사업

2026.10.

事項

횡 단 면 도

縮尺

1:50

A -